

Drawing List				
Sheet Number	Sheet Name	Drawn By	Checked By	Sheet Issue Date
A601	Details	PFA	DPM	07/07/20
G100	Cover	PFA	DPM	05/31/20
A101	Floor Plans	PFA	DPM	05/31/20
A102	Floor Plans	PFA	DPM	05/31/20
A201	Elevations	PFA	DPM	05/31/20
A202	Elevations	PFA	DPM	05/31/20
A203	Elevations	PFA	DPM	05/31/20
A301	Sections	PFA	DPM	05/31/20

# PAUL F. AUBIN CONSULTING SERVICES

[www.paulaubin.com](http://www.paulaubin.com)

[www.autodesk.com/revit](http://www.autodesk.com/revit)


Consultant  
Address  
Address  
Phone  
Fax  
e-mail

# Detailing and Annotation Residential Cover

ect number	2020.0
	8/1/202
n by	PF
cked by	DPM

# G100

e  $1'' = 10'^{-3}$

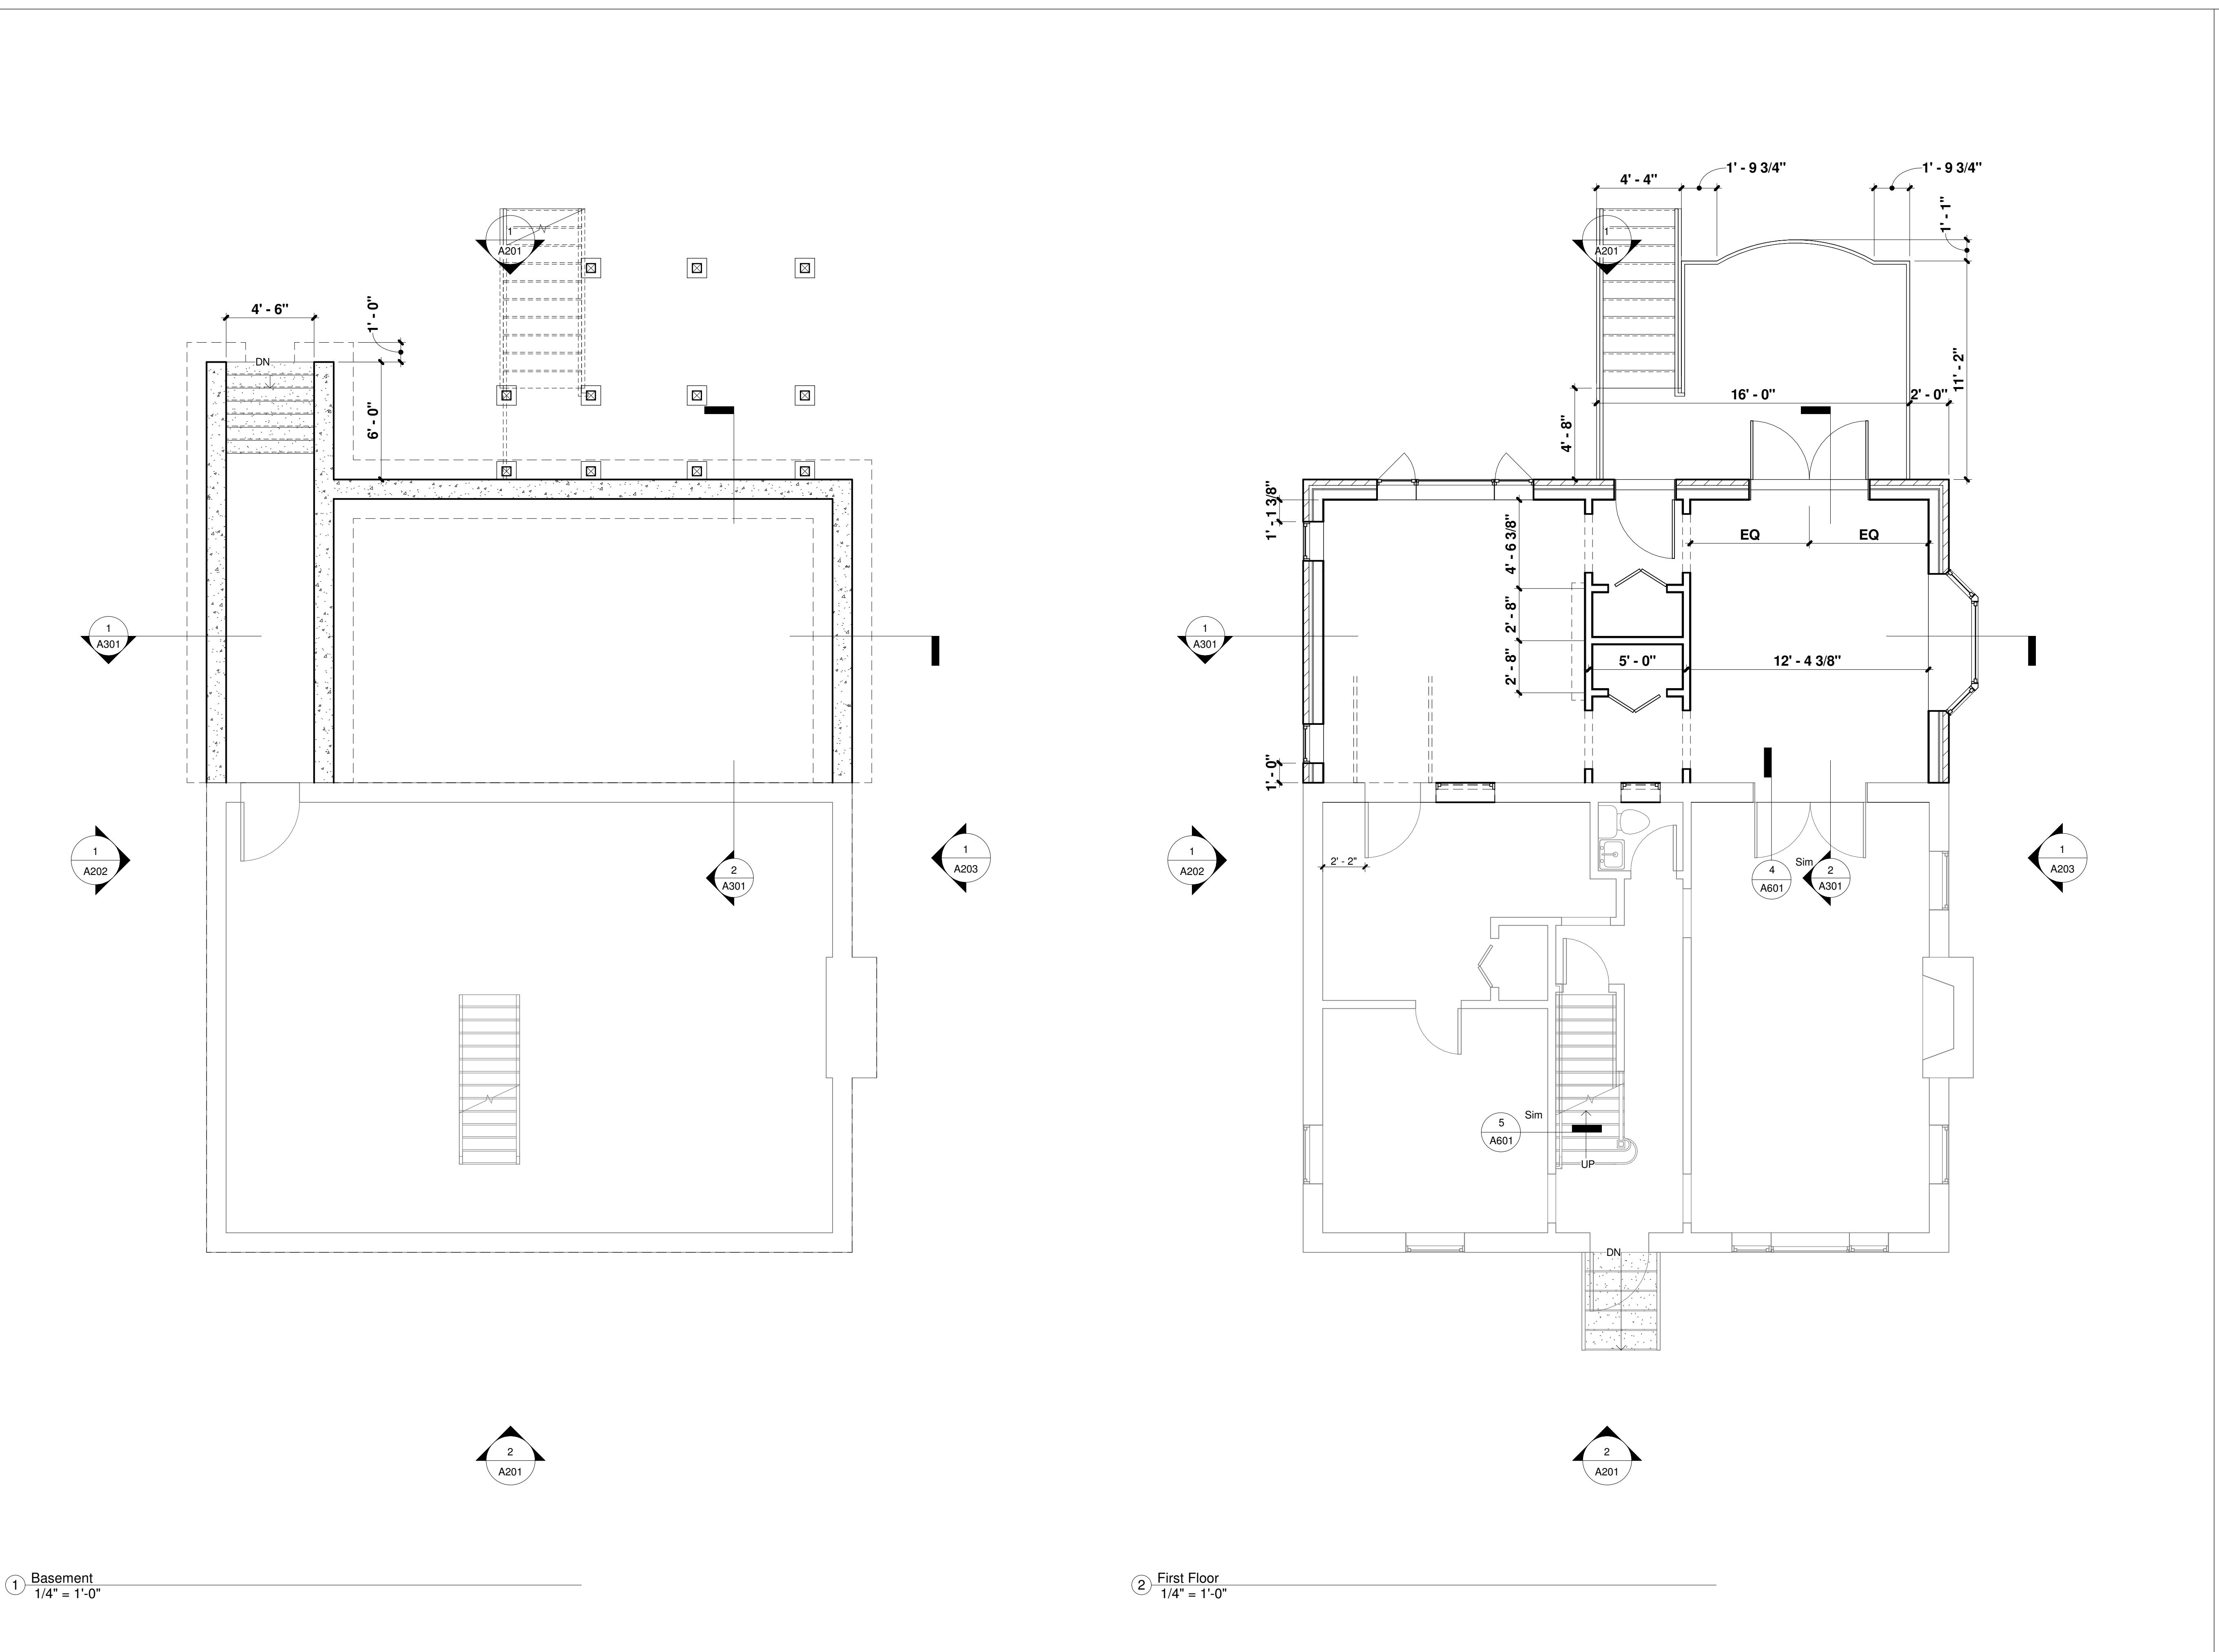

**PAUL F. AUBIN**  
CONSULTING SERVICES

[www.paulaubin.com](http://www.paulaubin.com)

[www.autodesk.com/revit](http://www.autodesk.com/revit)

l  
sultant  
ess  
ess  
ne  
  
il

l  
sultant  
ess  
ess  
ne  
il

l  
sultant  
ess  
ess  
ne  
il

l  
sultant  
ess  
ess  
ne  
ail

l  
sultant  
ess  
ess  
ne  
il

# Detailing and Annotation 12 Residential Floor Plans

Project number	2020.02
Date	8/1/2020
Signed by	PFA
Checked by	DPM

A101

ale  $1/4" = 1'-0"$



[www.paulaubin.com](http://www.paulaubin.com)

[www.autodesk.com/revit](http://www.autodesk.com/revit)

ultant  
ss  
ss  
e

ultant  
ss  
ss  
e

lnter  
ss  
ss  
e

ultant  
ss  
ss  
e

ultant  
ss  
ss  
e


# Detailing and Annotation 12 Residential Floor Plans

project number	2020.02
date	8/1/2020
rawn by	PFA
hecked by	DPM

A102



cale  $1/4" = 1'-0"$

7/11/2020 4:32:30 PM

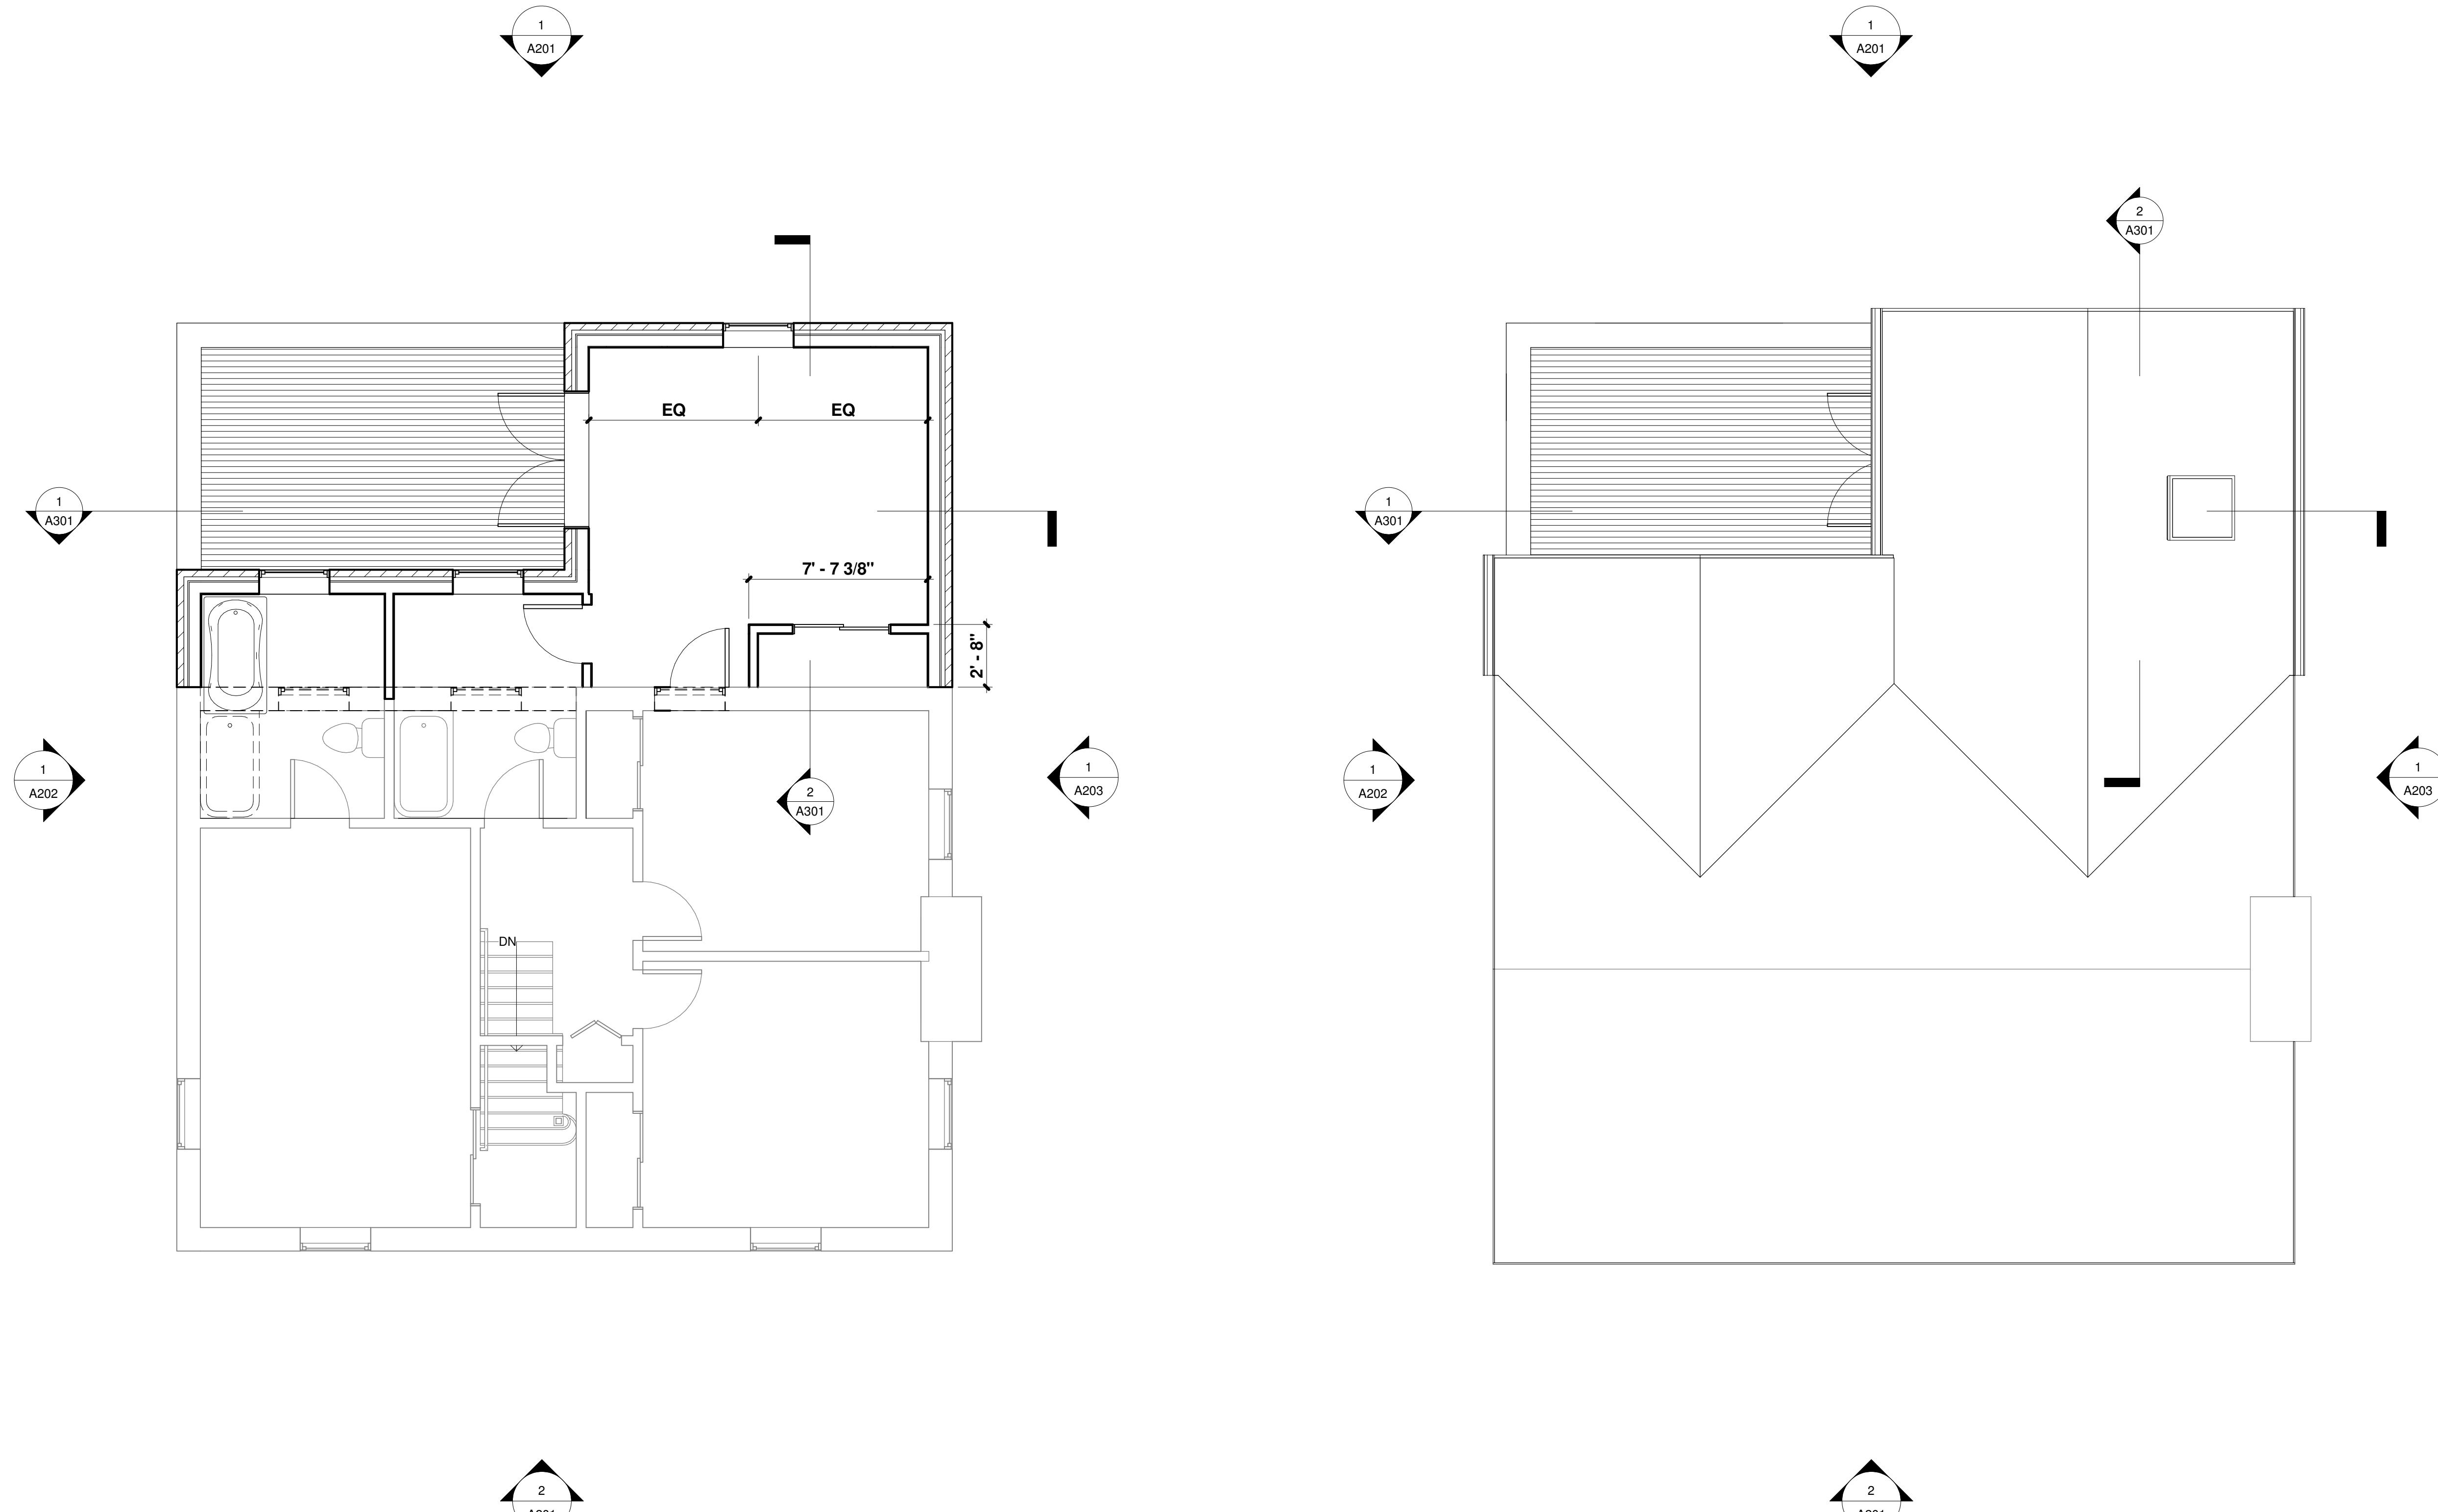

1 Second Floor  
1/4" = 1'-0"

2 Roof  
1/4" = 1'-0"

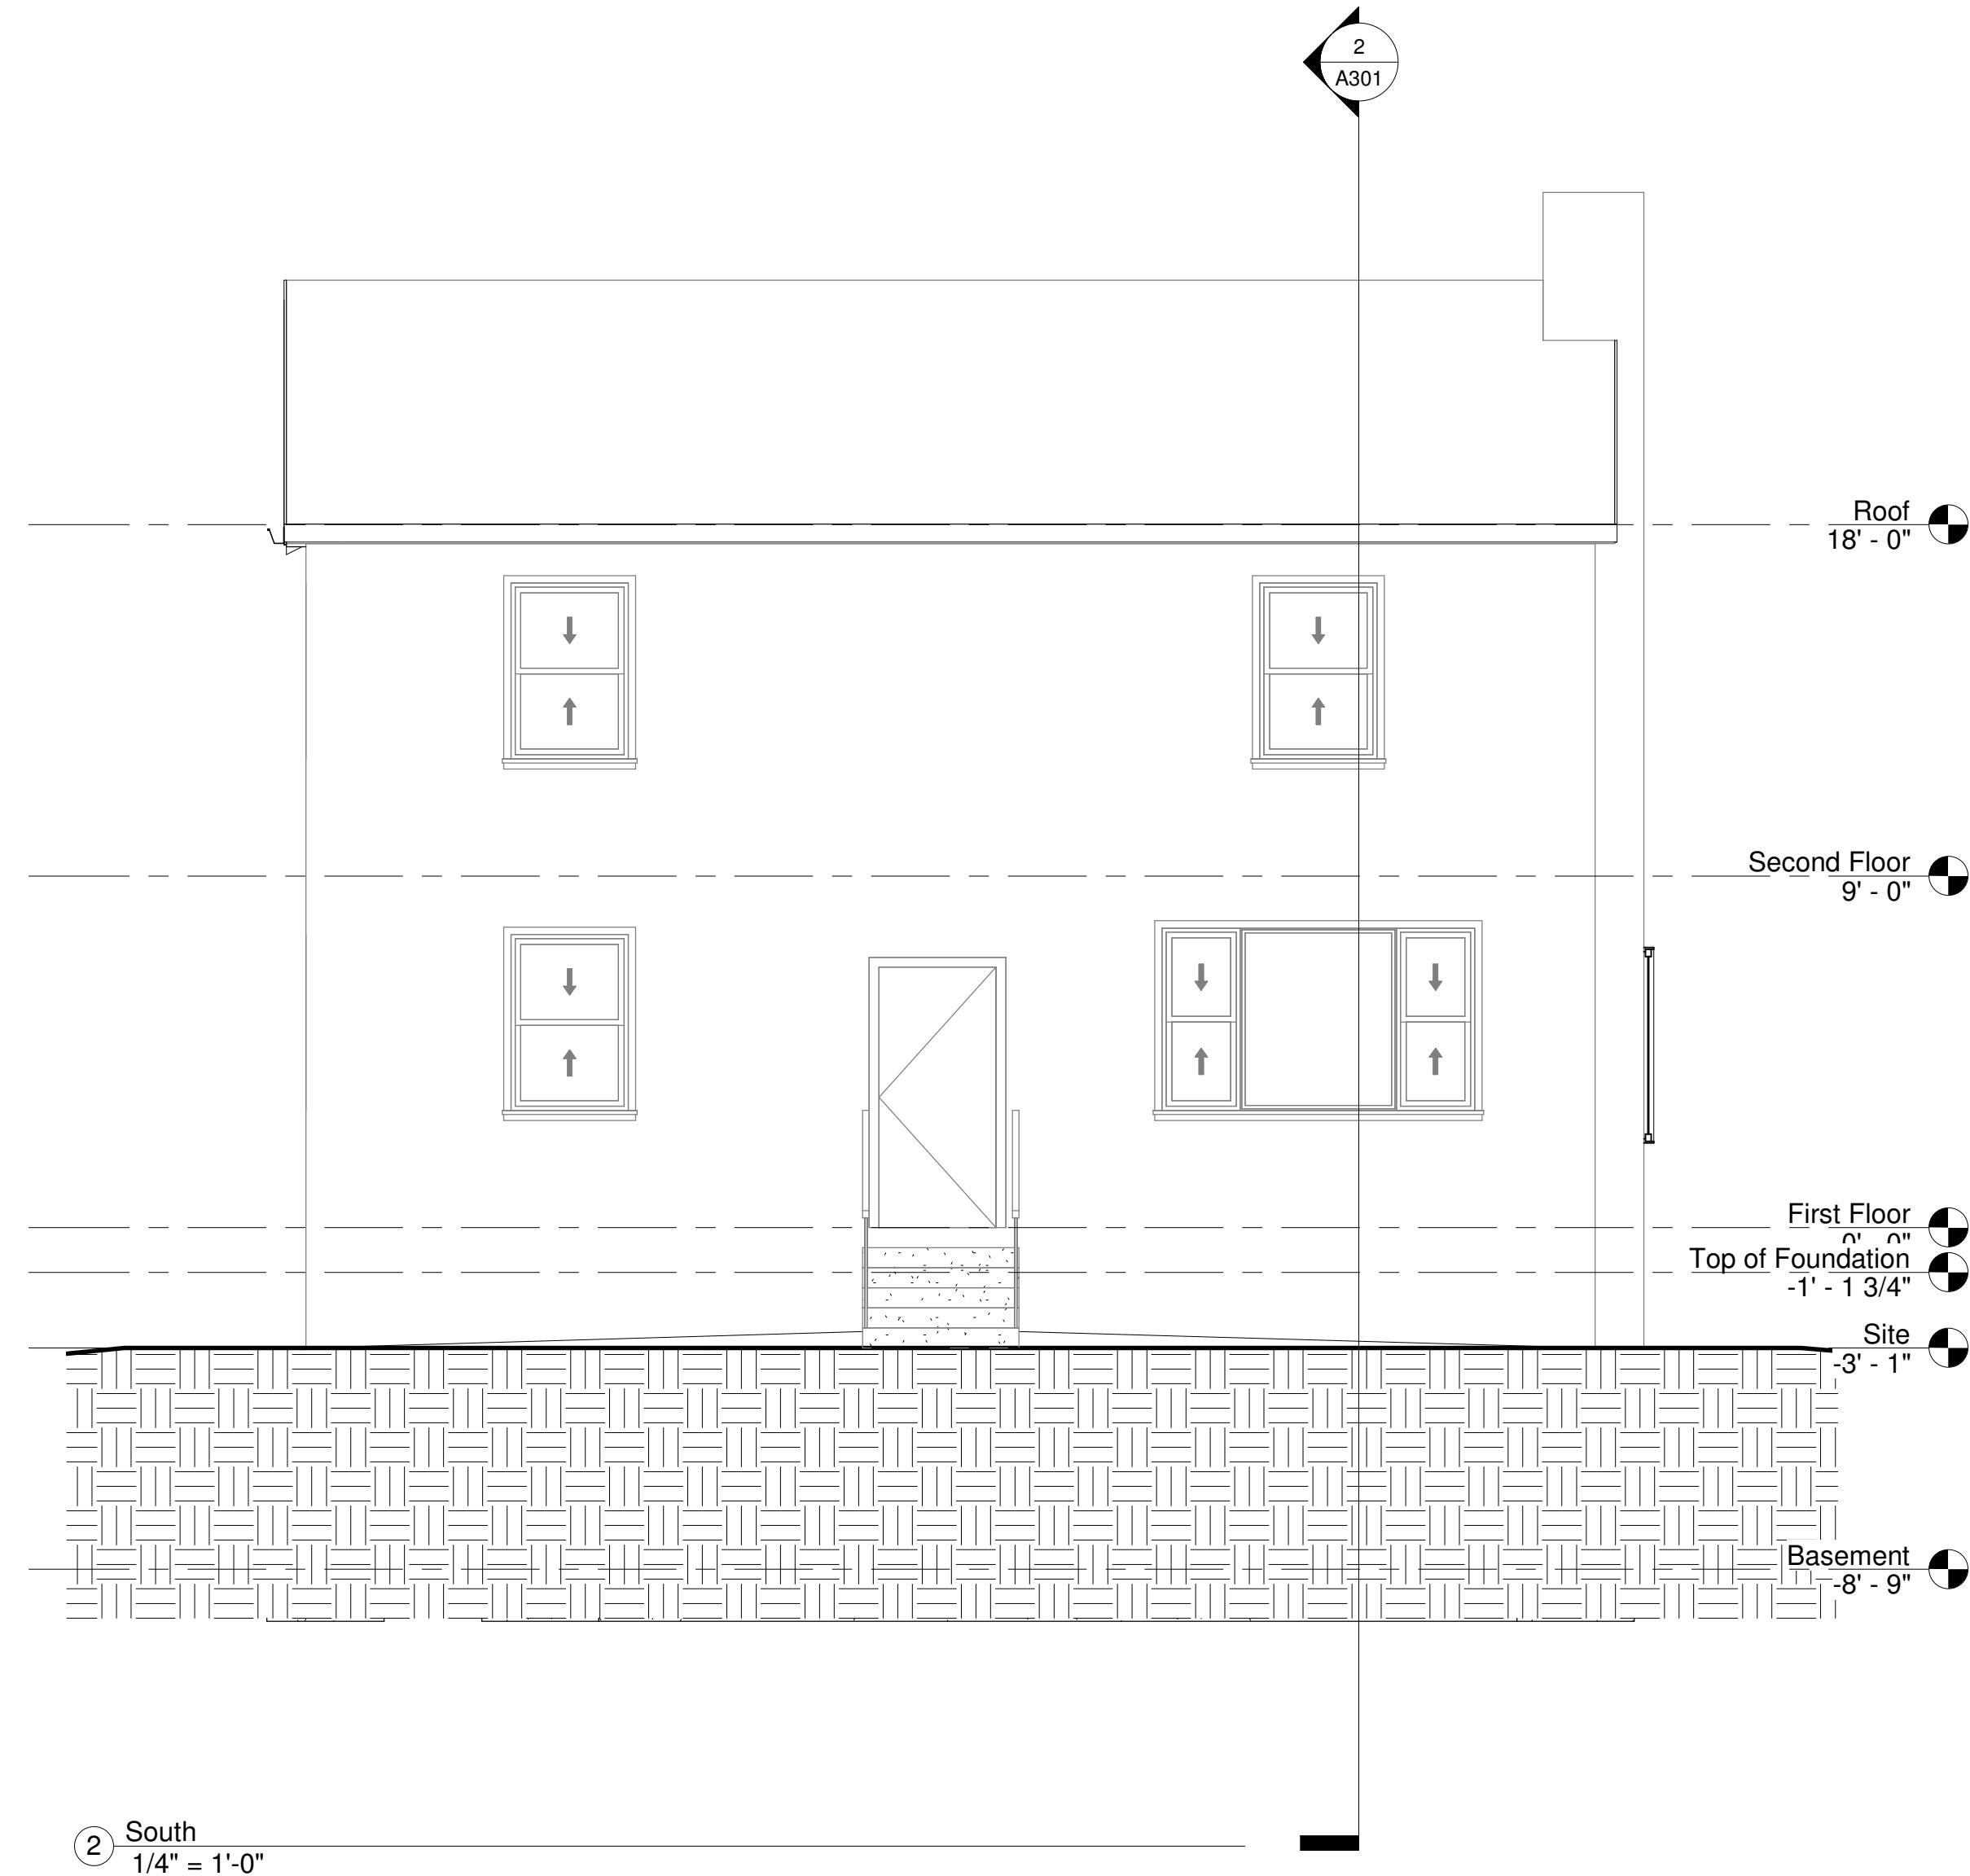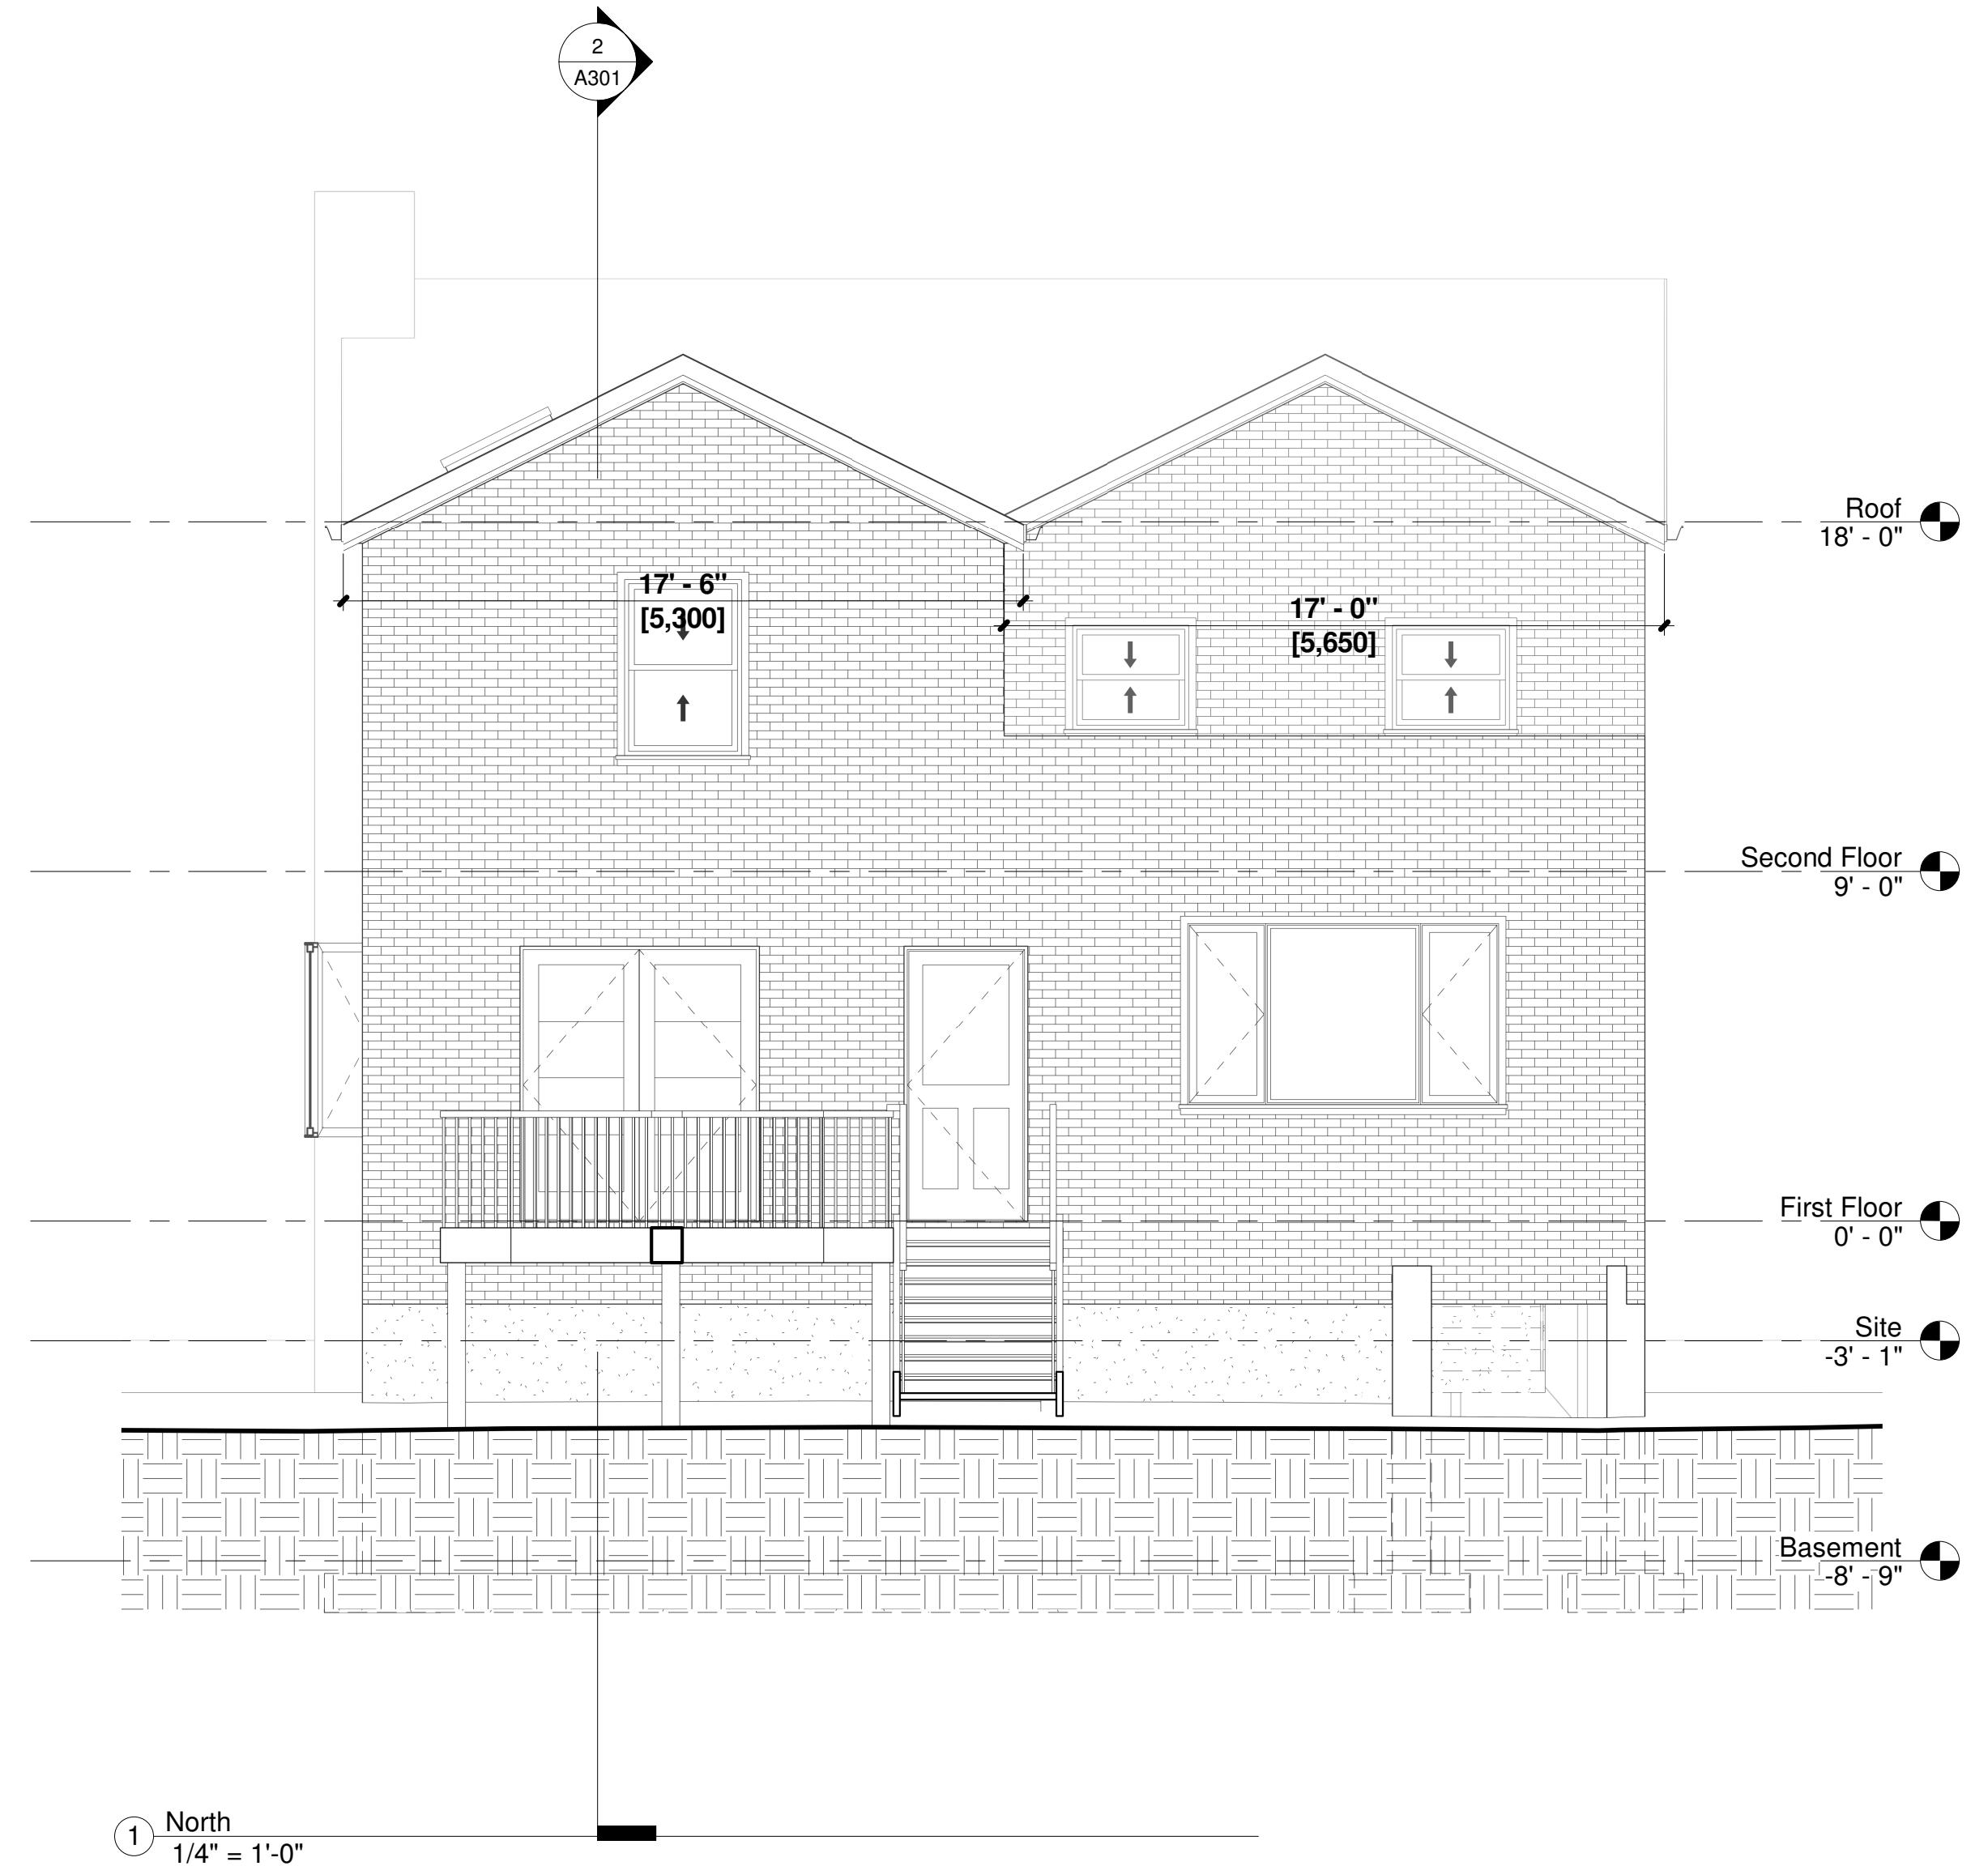

# PAUL F. AUBIN CONSULTING SERVICES

[www.paulaubin.com](http://www.paulaubin.com)

[www.autodesk.com/revit](http://www.autodesk.com/revit)

nsultant  
dress  
dress  
one  
x  
mail

nsultant  
dress  
dress  
one  
x  
nail

nsultant  
dress  
dress  
one  
x  
nail

nsultant  
dress  
dress  
one  
x  
nail

nsultant  
dress  
dress  
one  
x  
mail

# Detailing and Annotation 12 Residential Elevations

Project number	2020.0
Date	8/1/2022
Drawn by	PF
Checked by	DPM

A201

scale 1/4" = 1'-0"



[www.paulaubin.com](http://www.paulaubin.com)

[www.autodesk.com/revit](http://www.autodesk.com/revit)

nsultant  
dress  
dress  
one  
x  
mail

nsultant  
dress  
dress  
one  
x  
nail

# Detailing and Annotation 12 Residential Elevations

Project number	2020.02
Date	8/1/2020
Drawn by	PFA
Checked by	DPM

A202

Scale 1/4" = 1'-0"



[www.paulaubin.com](http://www.paulaubin.com)

[www.autodesk.com/revit](http://www.autodesk.com/revit)

ultant  
ss  
ss  
e

ultant  
ss  
ss  
e

ultant  
ss  
ss  
e

lnter  
ss  
ss  
e

ultant  
ss  
ss  
e

# Detailing and Annotation 12 Residential Elevations

Project number	2020.02
Date	8/1/2020
Drawn by	PFA
Checked by	DPM

A203

scale **1/4" = 1'-0"**

7/11/2020 4:32:37 PM



**PAUL F. AUBIN**  
CONSULTING SERVICES

[www.paulaubin.com](http://www.paulaubin.com)

[www.autodesk.com/revit](http://www.autodesk.com/revit)

l  
sultant  
ess  
ess  
ne  
il

l  
sultant  
ess  
ess  
ne  
ail

l  
sultant  
ess  
ess  
ne  
il

l  
sultant  
ess  
ess  
ne  
ail


l  
sultant  
ess  
ess  
ne  
il

# Detailing and Annotation 12 Residential Sections

Project number	2020.02
Date	8/1/2020
Drawn by	PFA
Checked by	DPM


A301

Scale **1/4" = 1'-0"**

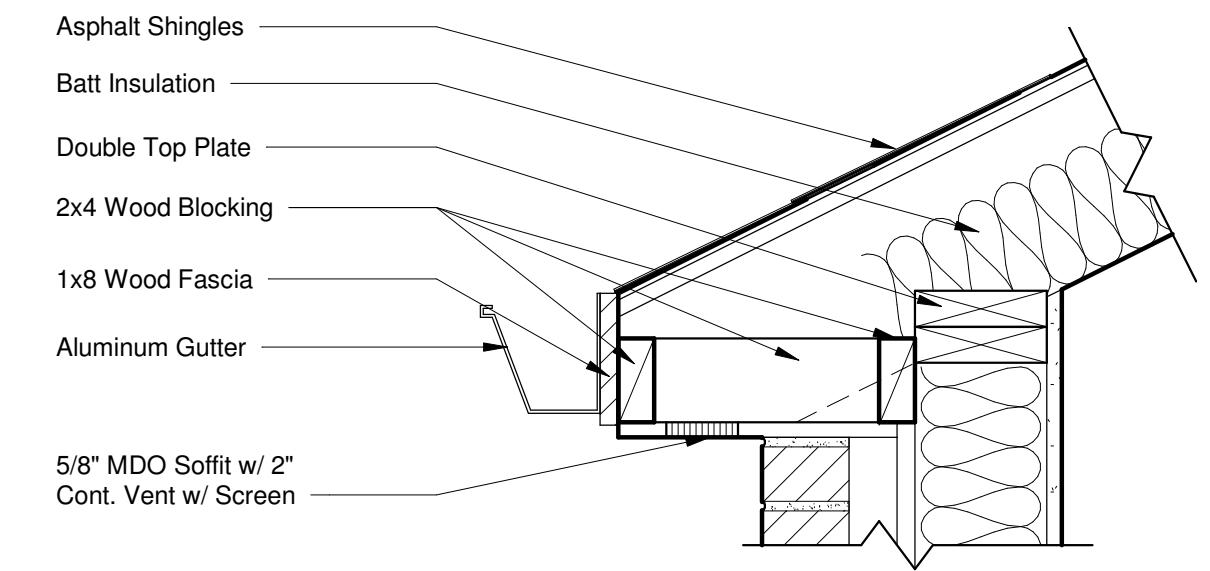


**3 Typical Eave Condition**

$$-1/2 = -0$$

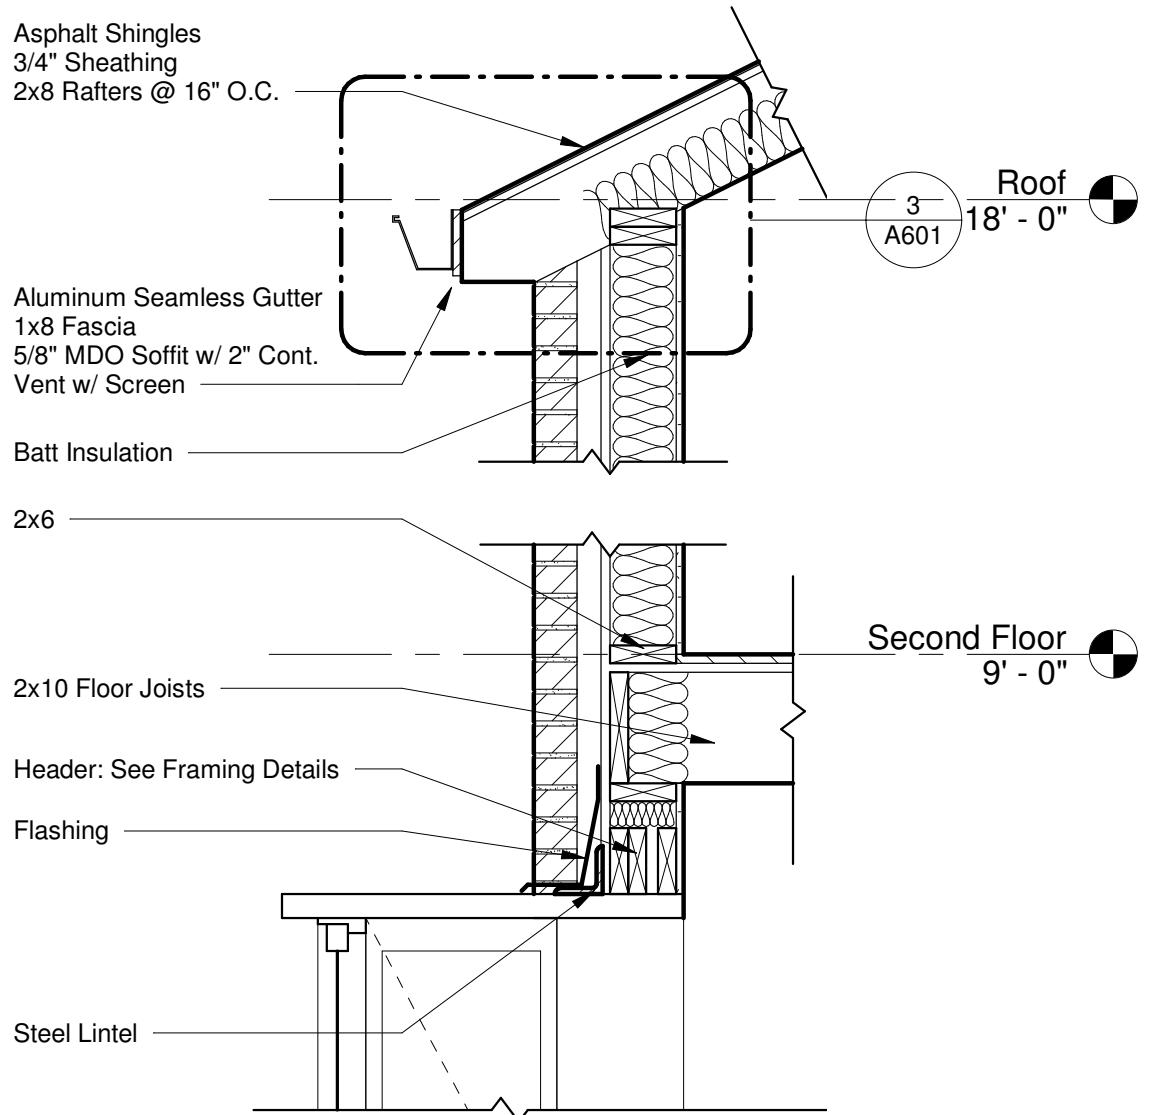


**2 Wall Section at Second Floor  
3/4" - 1'-0"**

$$\textcircled{E} \quad 3/4" = 1'-0"$$

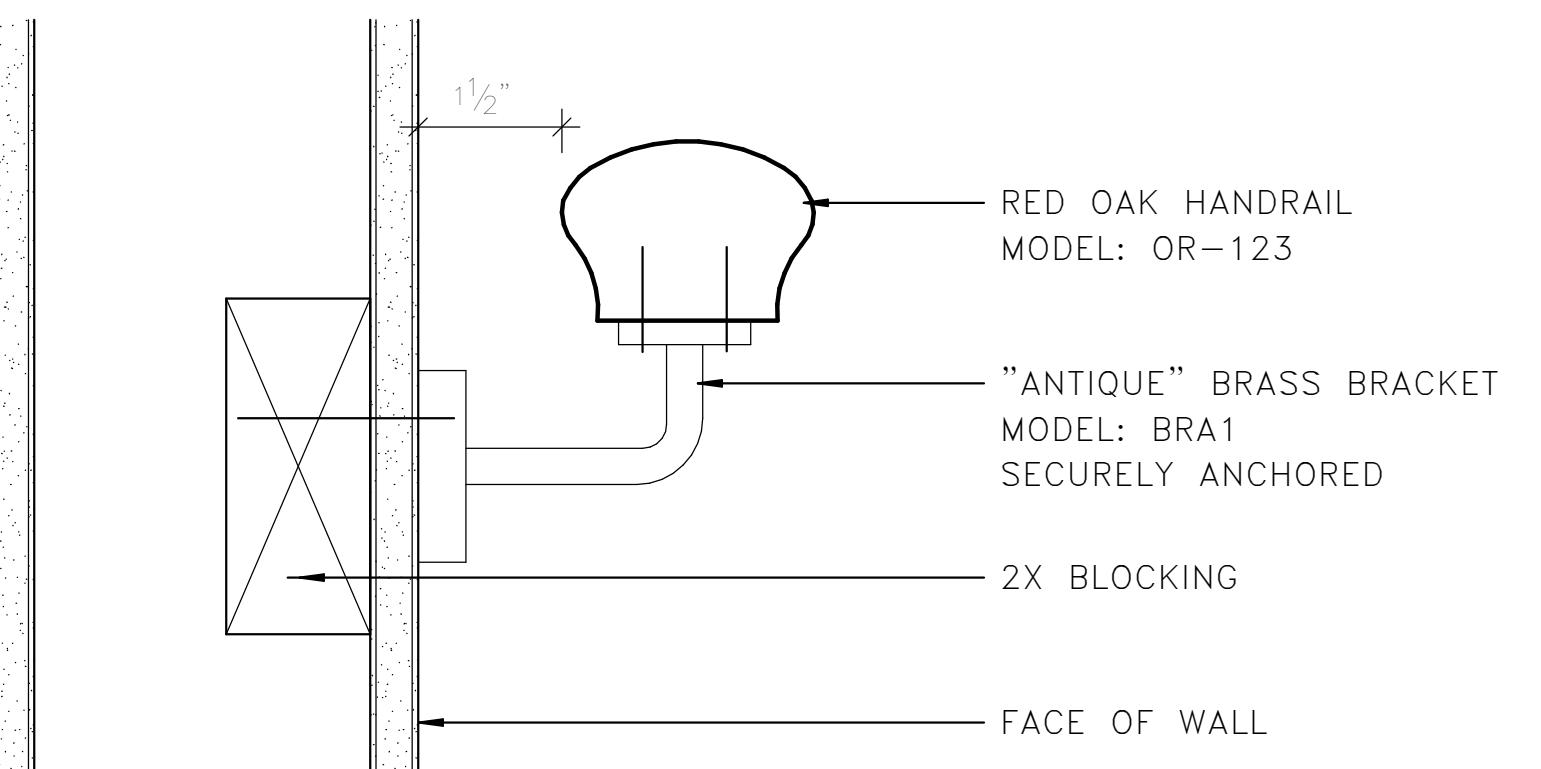


5 New Railing Detail  
6" - 11' 0"

**5**      Now I know  
6" = 1'-0"

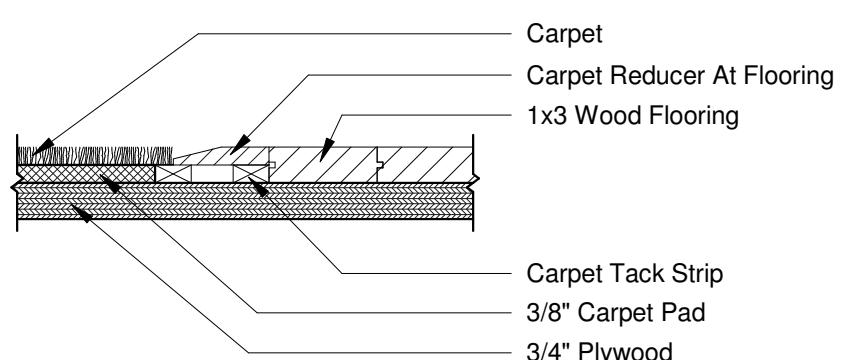

## 4 Typical Floor Transition Detail

4 Typical  
3" = 1'-0"

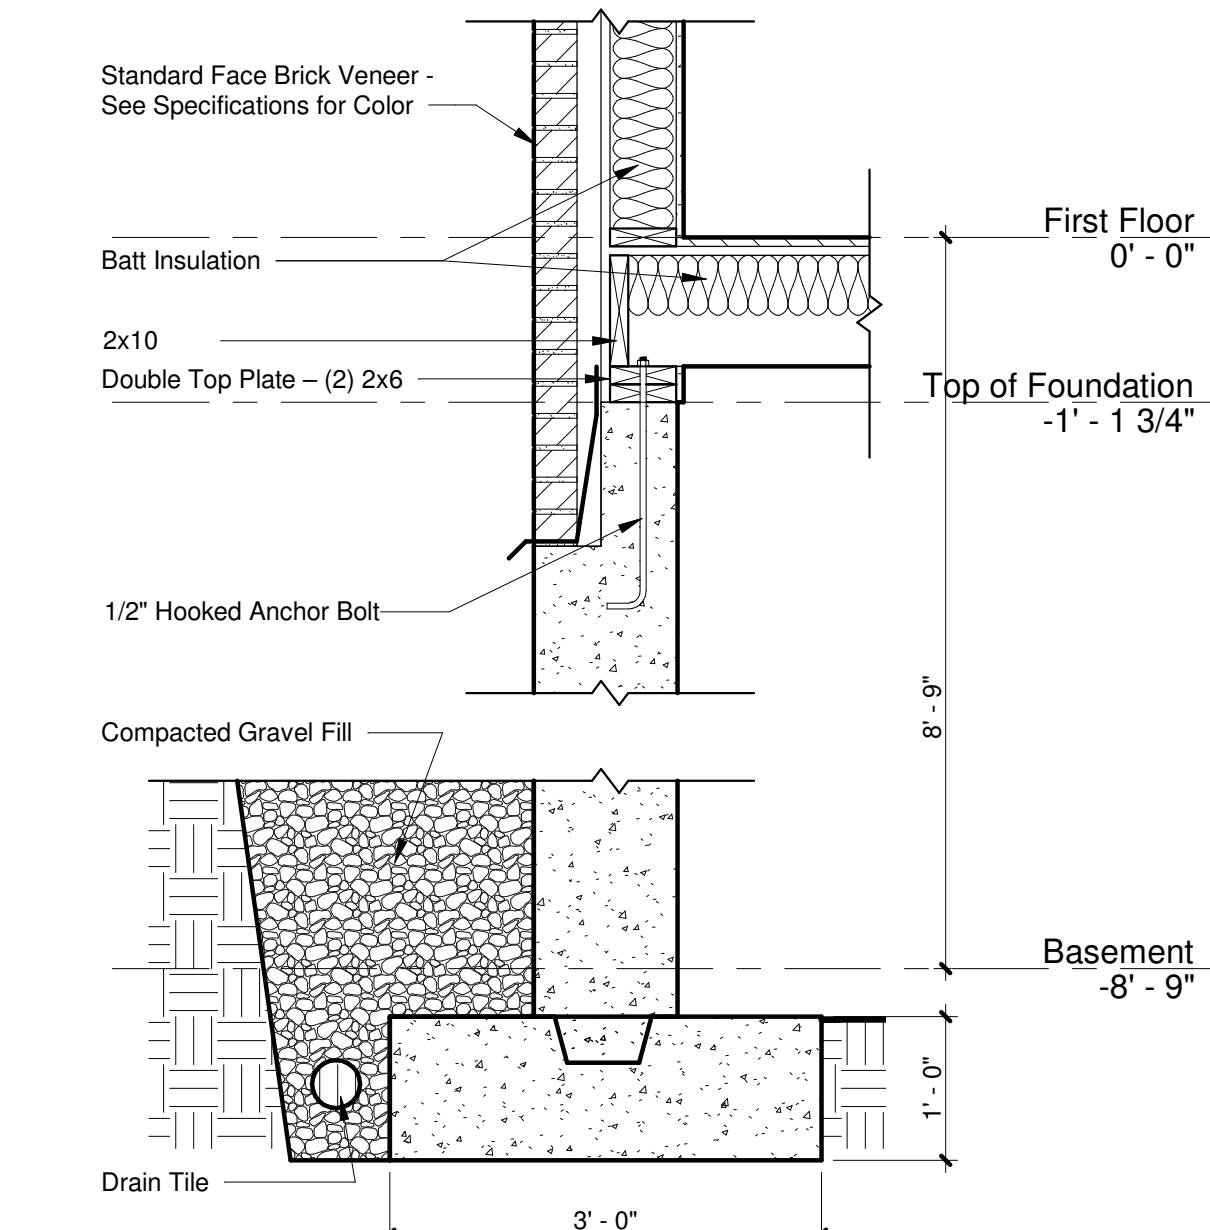

## 1 Typical Wall Foundation Detail

1      Typical value  
3/4" = 1"

# Detailing and Annotation 12 Residential Details

project number	2020.02
date	8/1/2020
rawn by	Author
hecked by	Checker

A601

As indicated