


15 Commercial

123 State ST
Suite 201
Chicago, IL 60606
Printing and Output
8/1/2020

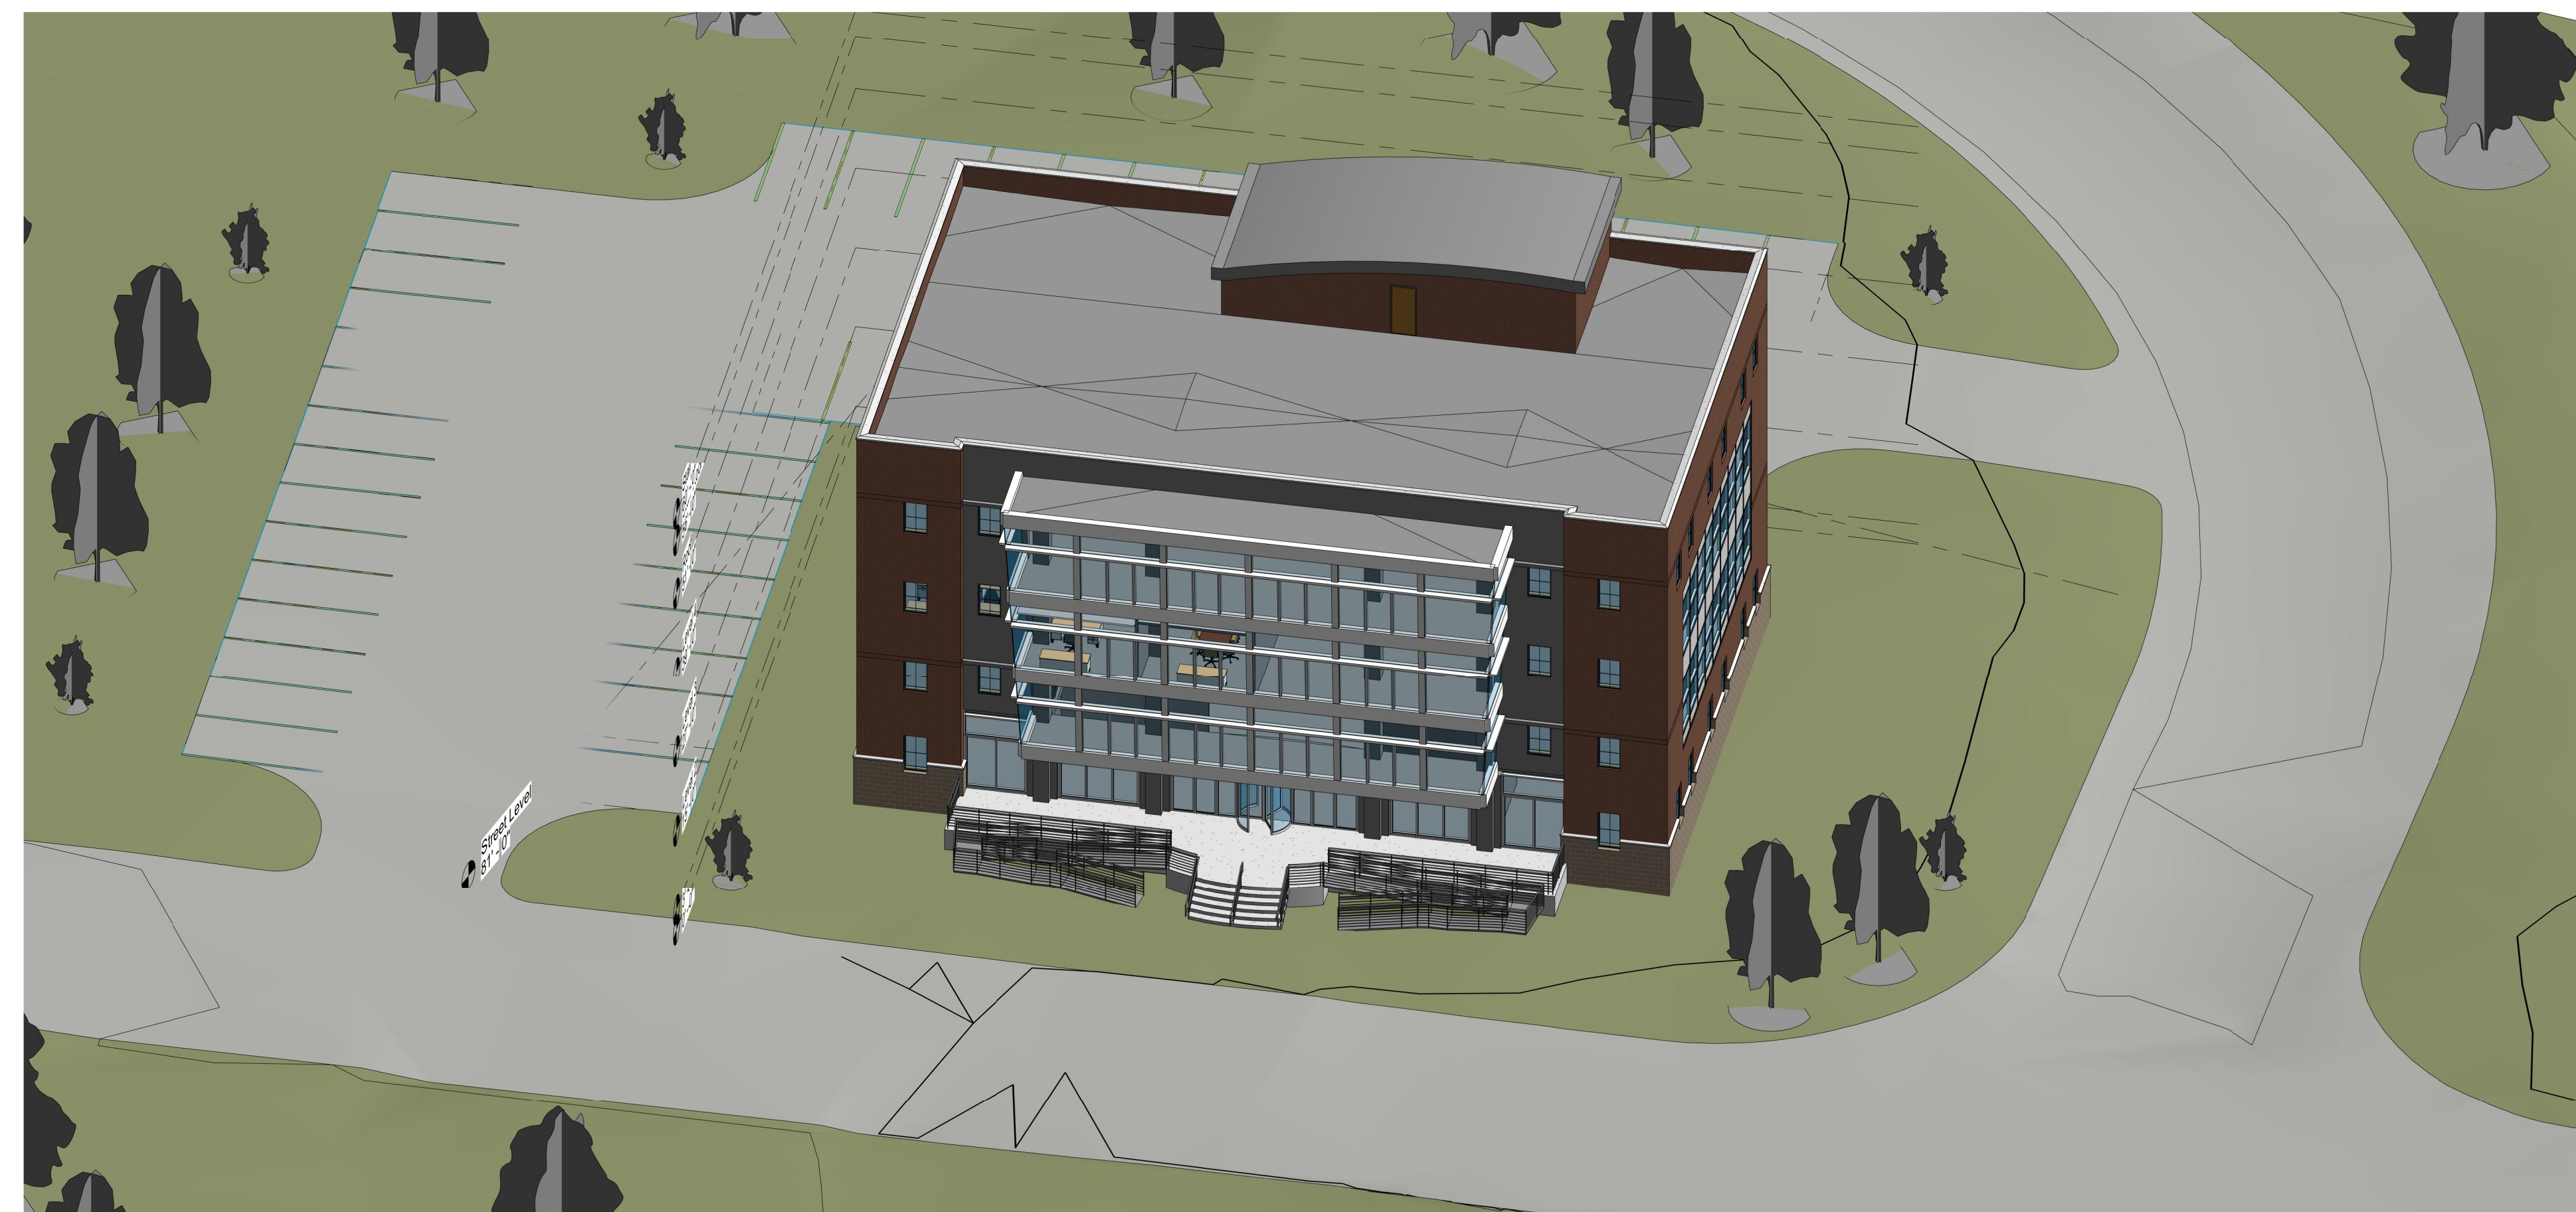

PA PAUL F. AUBIN
CONSULTING SERVICES

www.paulaubin.com

BIM Design Group
555 Revit DR
Suite 101
Chicago, IL
(555) 123-4567

Revit Consultant
777 MEP Way
Suite 101
Chicago, IL
(555) 765-4321


Location Map:

Drawing Index:

Sheet Number	Sheet Name	Sheet Issue Date
G100	Cover	05/27/20
A100	Architectural Site Plan	05/27/20
A101	Floor Plans	05/27/20
A102	Floor Plans	05/27/20
A103	Floor Plans	05/27/20
A104	Floor Plans	05/27/20
A105	Roof Plan	05/27/20
A111	Reflected Ceiling Plans	05/27/20
A112	Reflected Ceiling Plans	05/27/20
A113	Reflected Ceiling Plans	05/27/20

Sheet Number	Sheet Name	Sheet Issue Date
A114	Reflected Ceiling Plans	05/27/20
A201	Building Elevations	05/27/20
A202	Building Elevations	05/27/20
A301	Building Sections	05/27/20
A401	Interior Elevations	07/11/20
A601	Schedules	05/27/20
A602	Schedules	07/08/20
A603	Schedules	07/08/20
ASK1	Level 3 East	07/11/20
ASK2	Level 3 West	07/11/20

Architect's Seal:

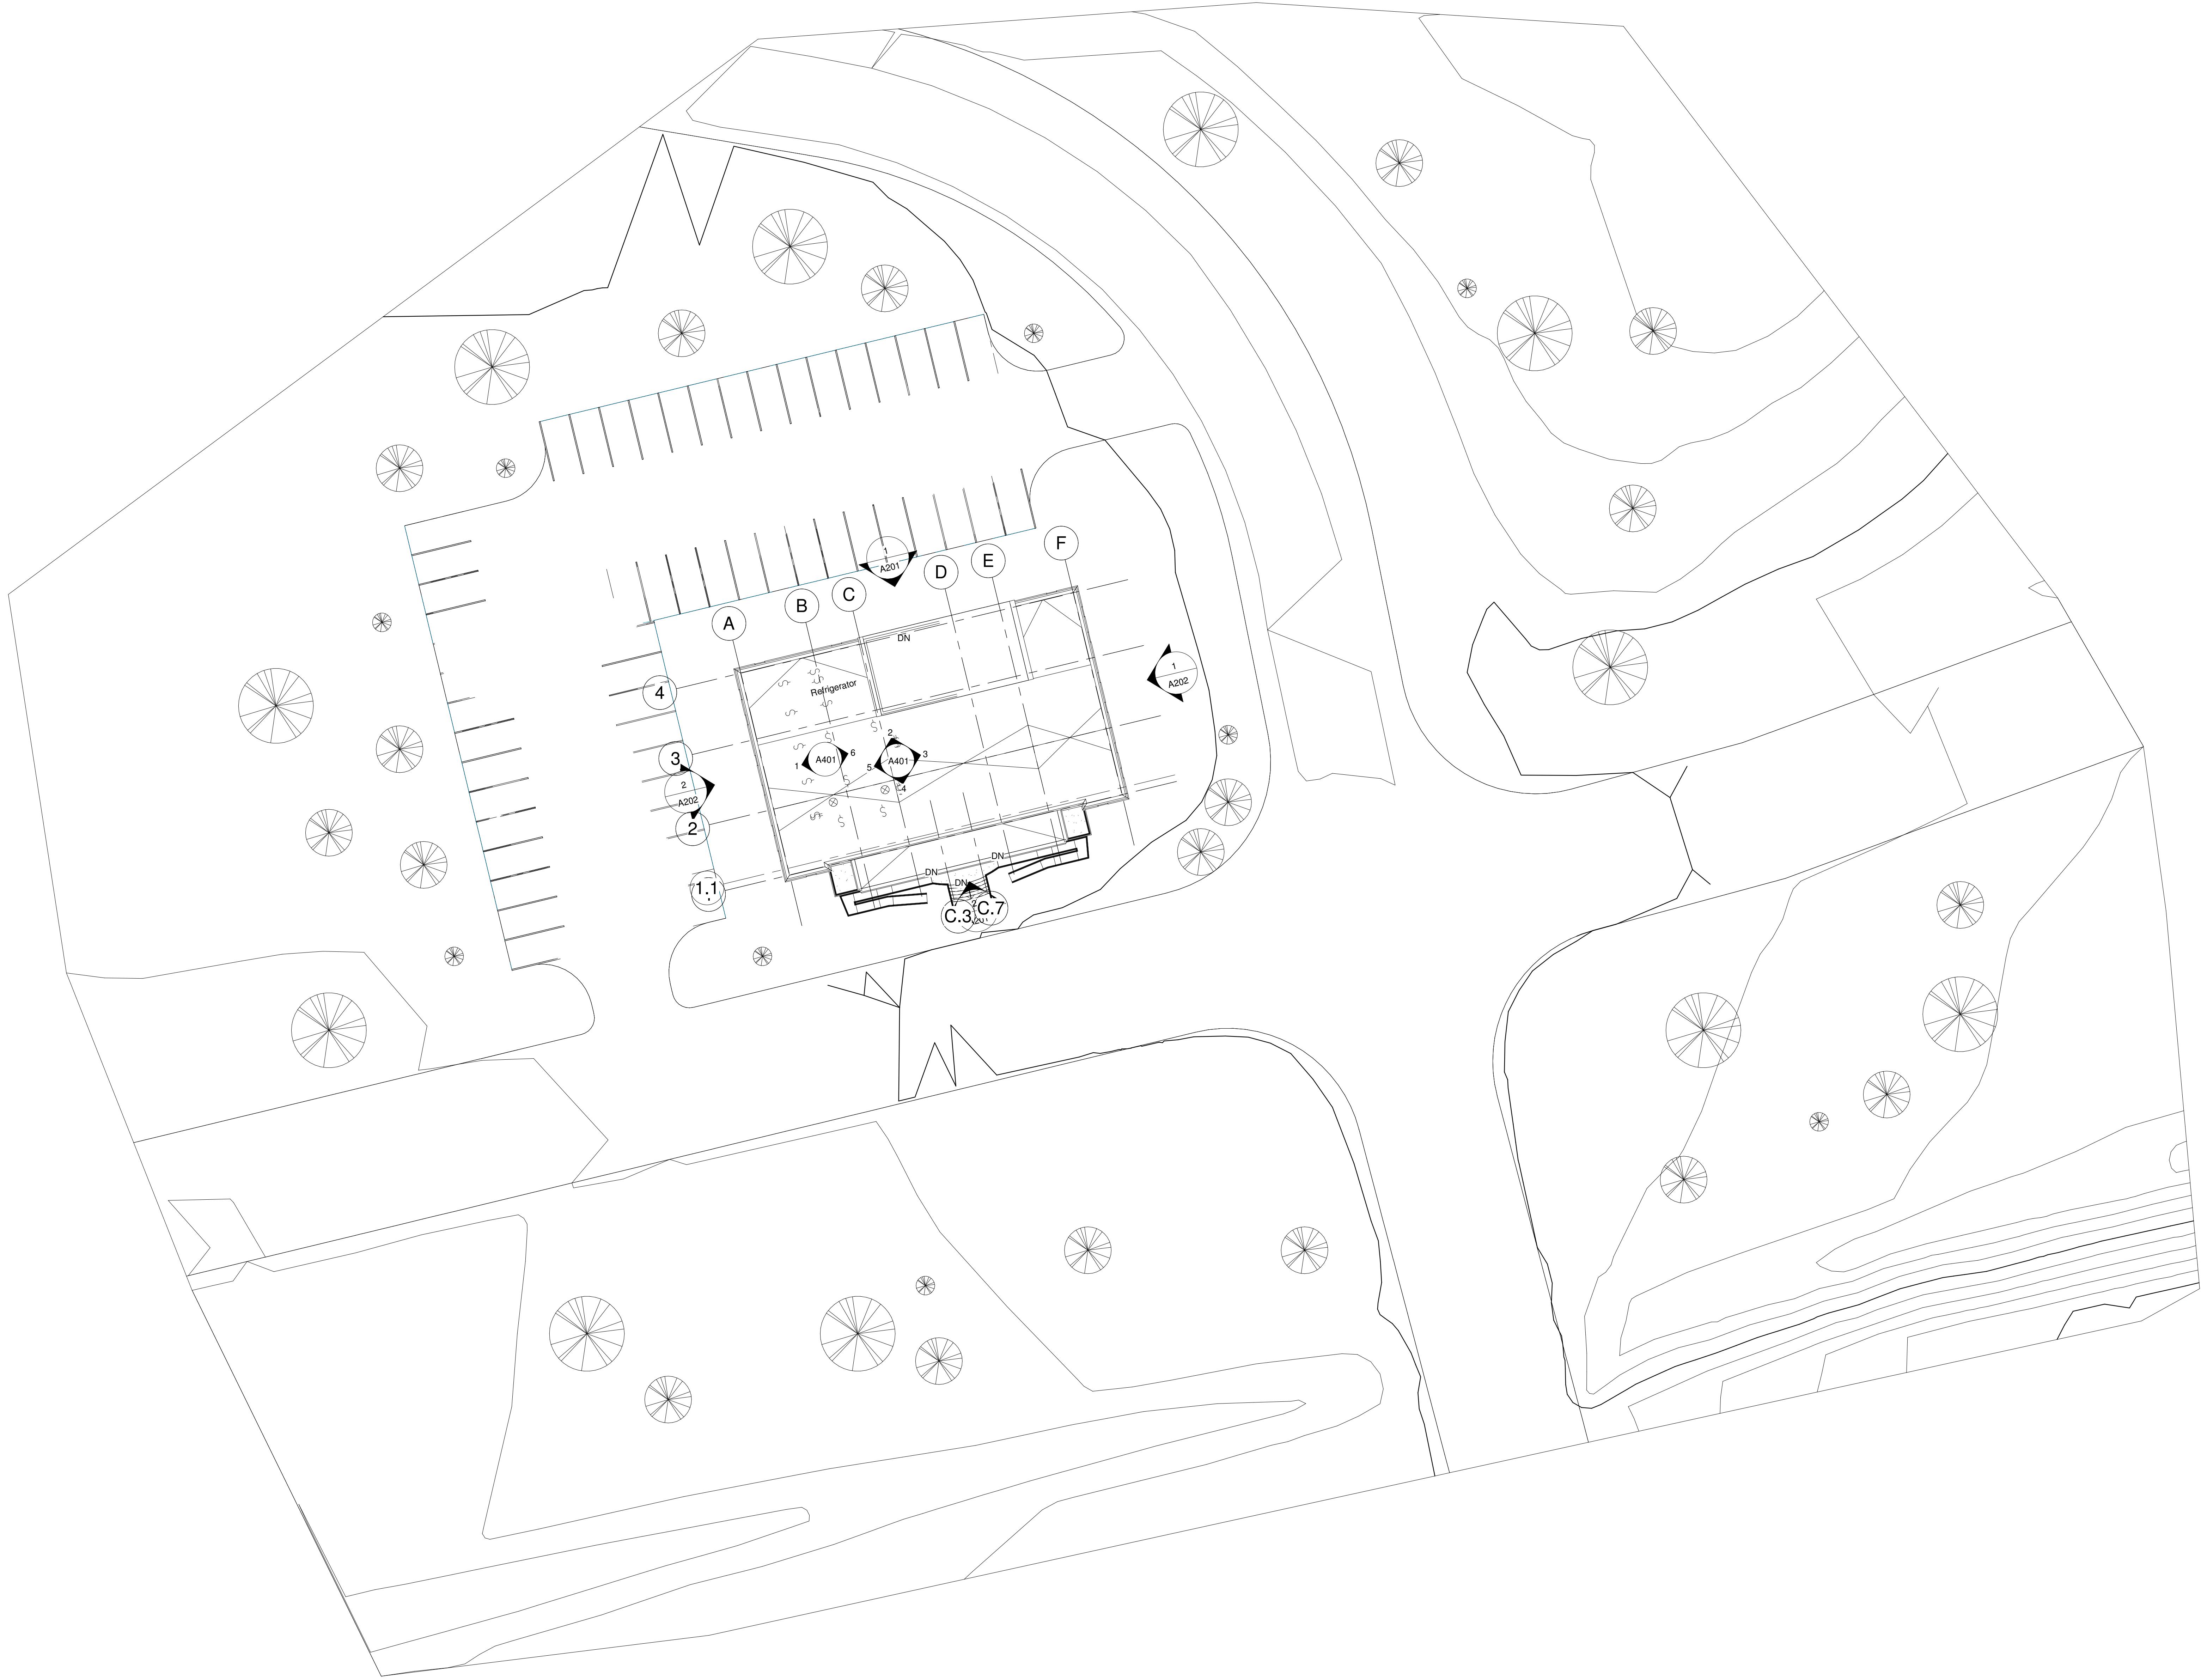

1 Architectural Site Plan
1" = 20'-0"



PAUL F. AUBIN CONSULTING SERVICES

www.paulaubin.com

www.autodesk.com/revit

Consultant
Address
Address
Address
Phone

Printing and Output

15 Commercial Architectural Site Plan

Project Number	2020.01A
Date	8/1/2020
Drawn By	PFA
Checked By	DPM

A100

1" = 20'-0"



www.paulaubin.com

www.autodesk.com/revit

Consultant
Address
Address
Address
Phone

Printing and Output

15 Commercial Floor Plans

Project Number	2020.01A
Date	8/1/2020
Drawn By	PFA
Checked By	DPM

A101

1/8" = 1'-0"

7/11/2020 4:26:43 PM



www.paulaubin.com

www.autodesk.com/revit

Consultant
Address
Address
Address
Phone

Printing and Output

15 Commercial Floor Plans

Project Number	2020.01A
Date	8/1/2020
Drawn By	PFA
Checked By	DPM

A102


e $1/8"$ = $1'-0"$

7/11/2020 4:26:44 PM



www.paulaubin.com

www.autodesk.com/revit

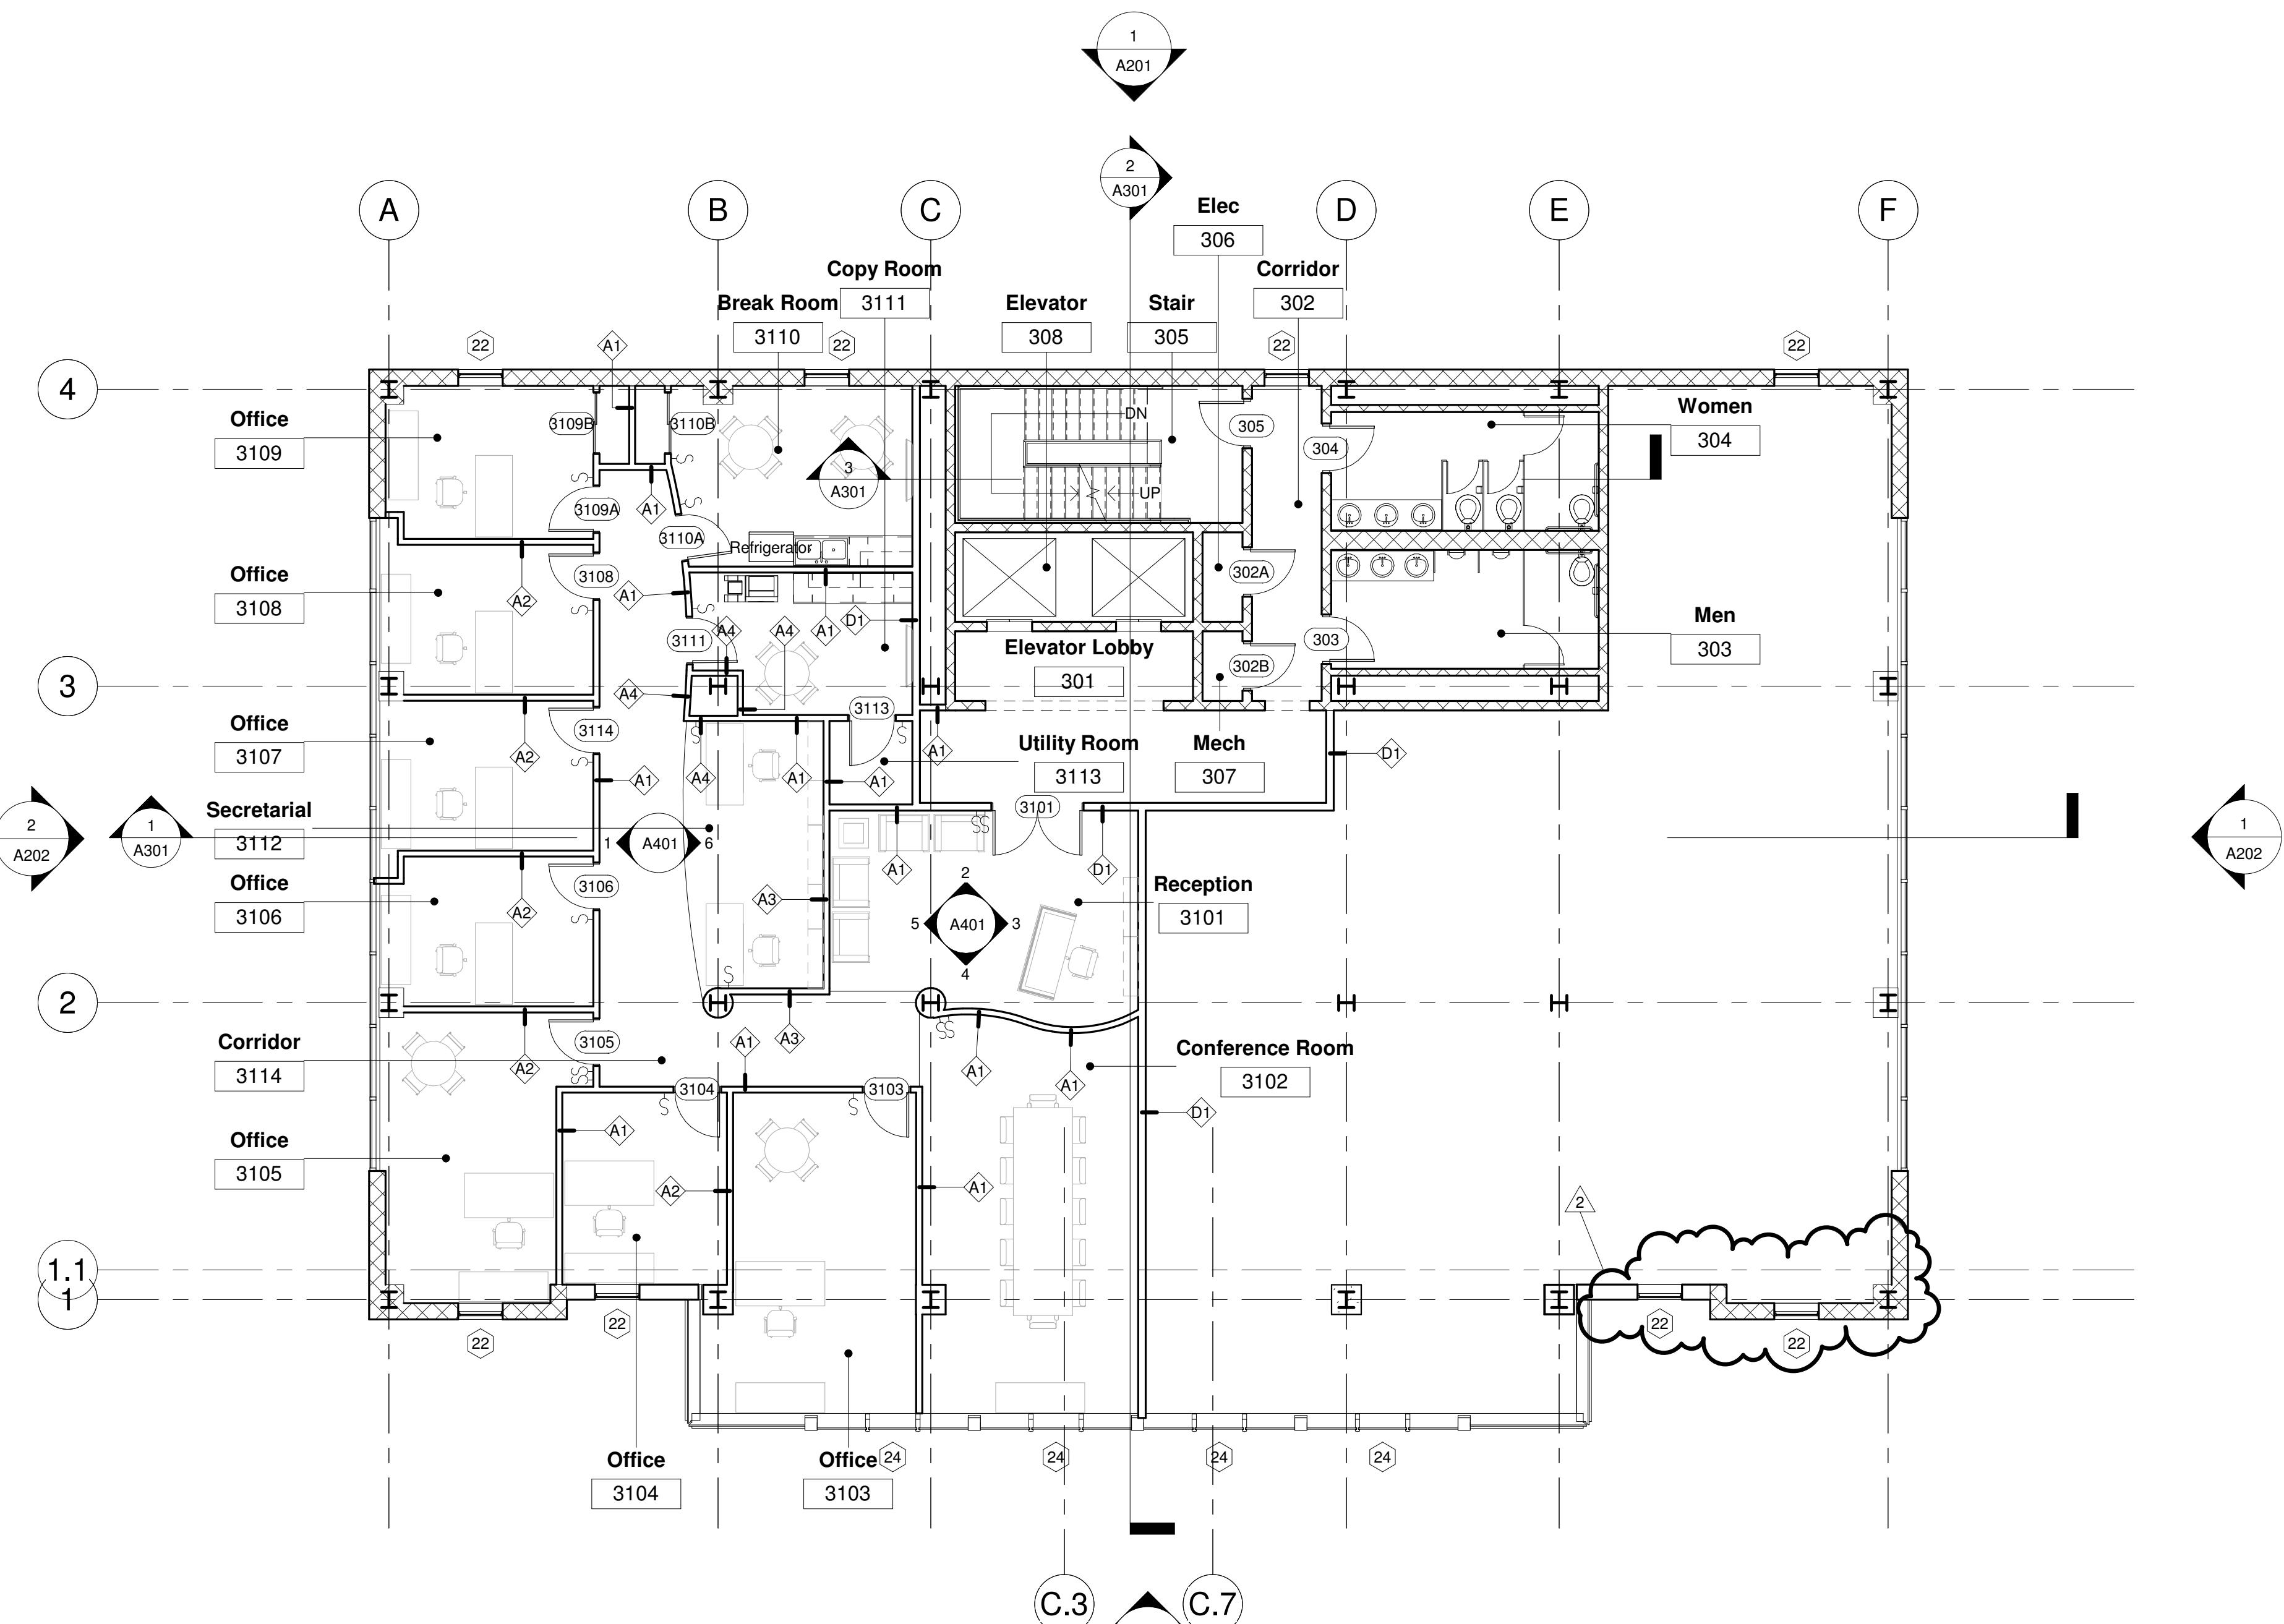

1 Third Floor Plan
1/8" = 1'-0"


Printing and Output

15 Commercial Floor Plans

Project Number	2020.01A
Date	8/1/2020
Drawn By	PFA
Checked By	DPM

A103

$$1/8" = 1'-0"$$

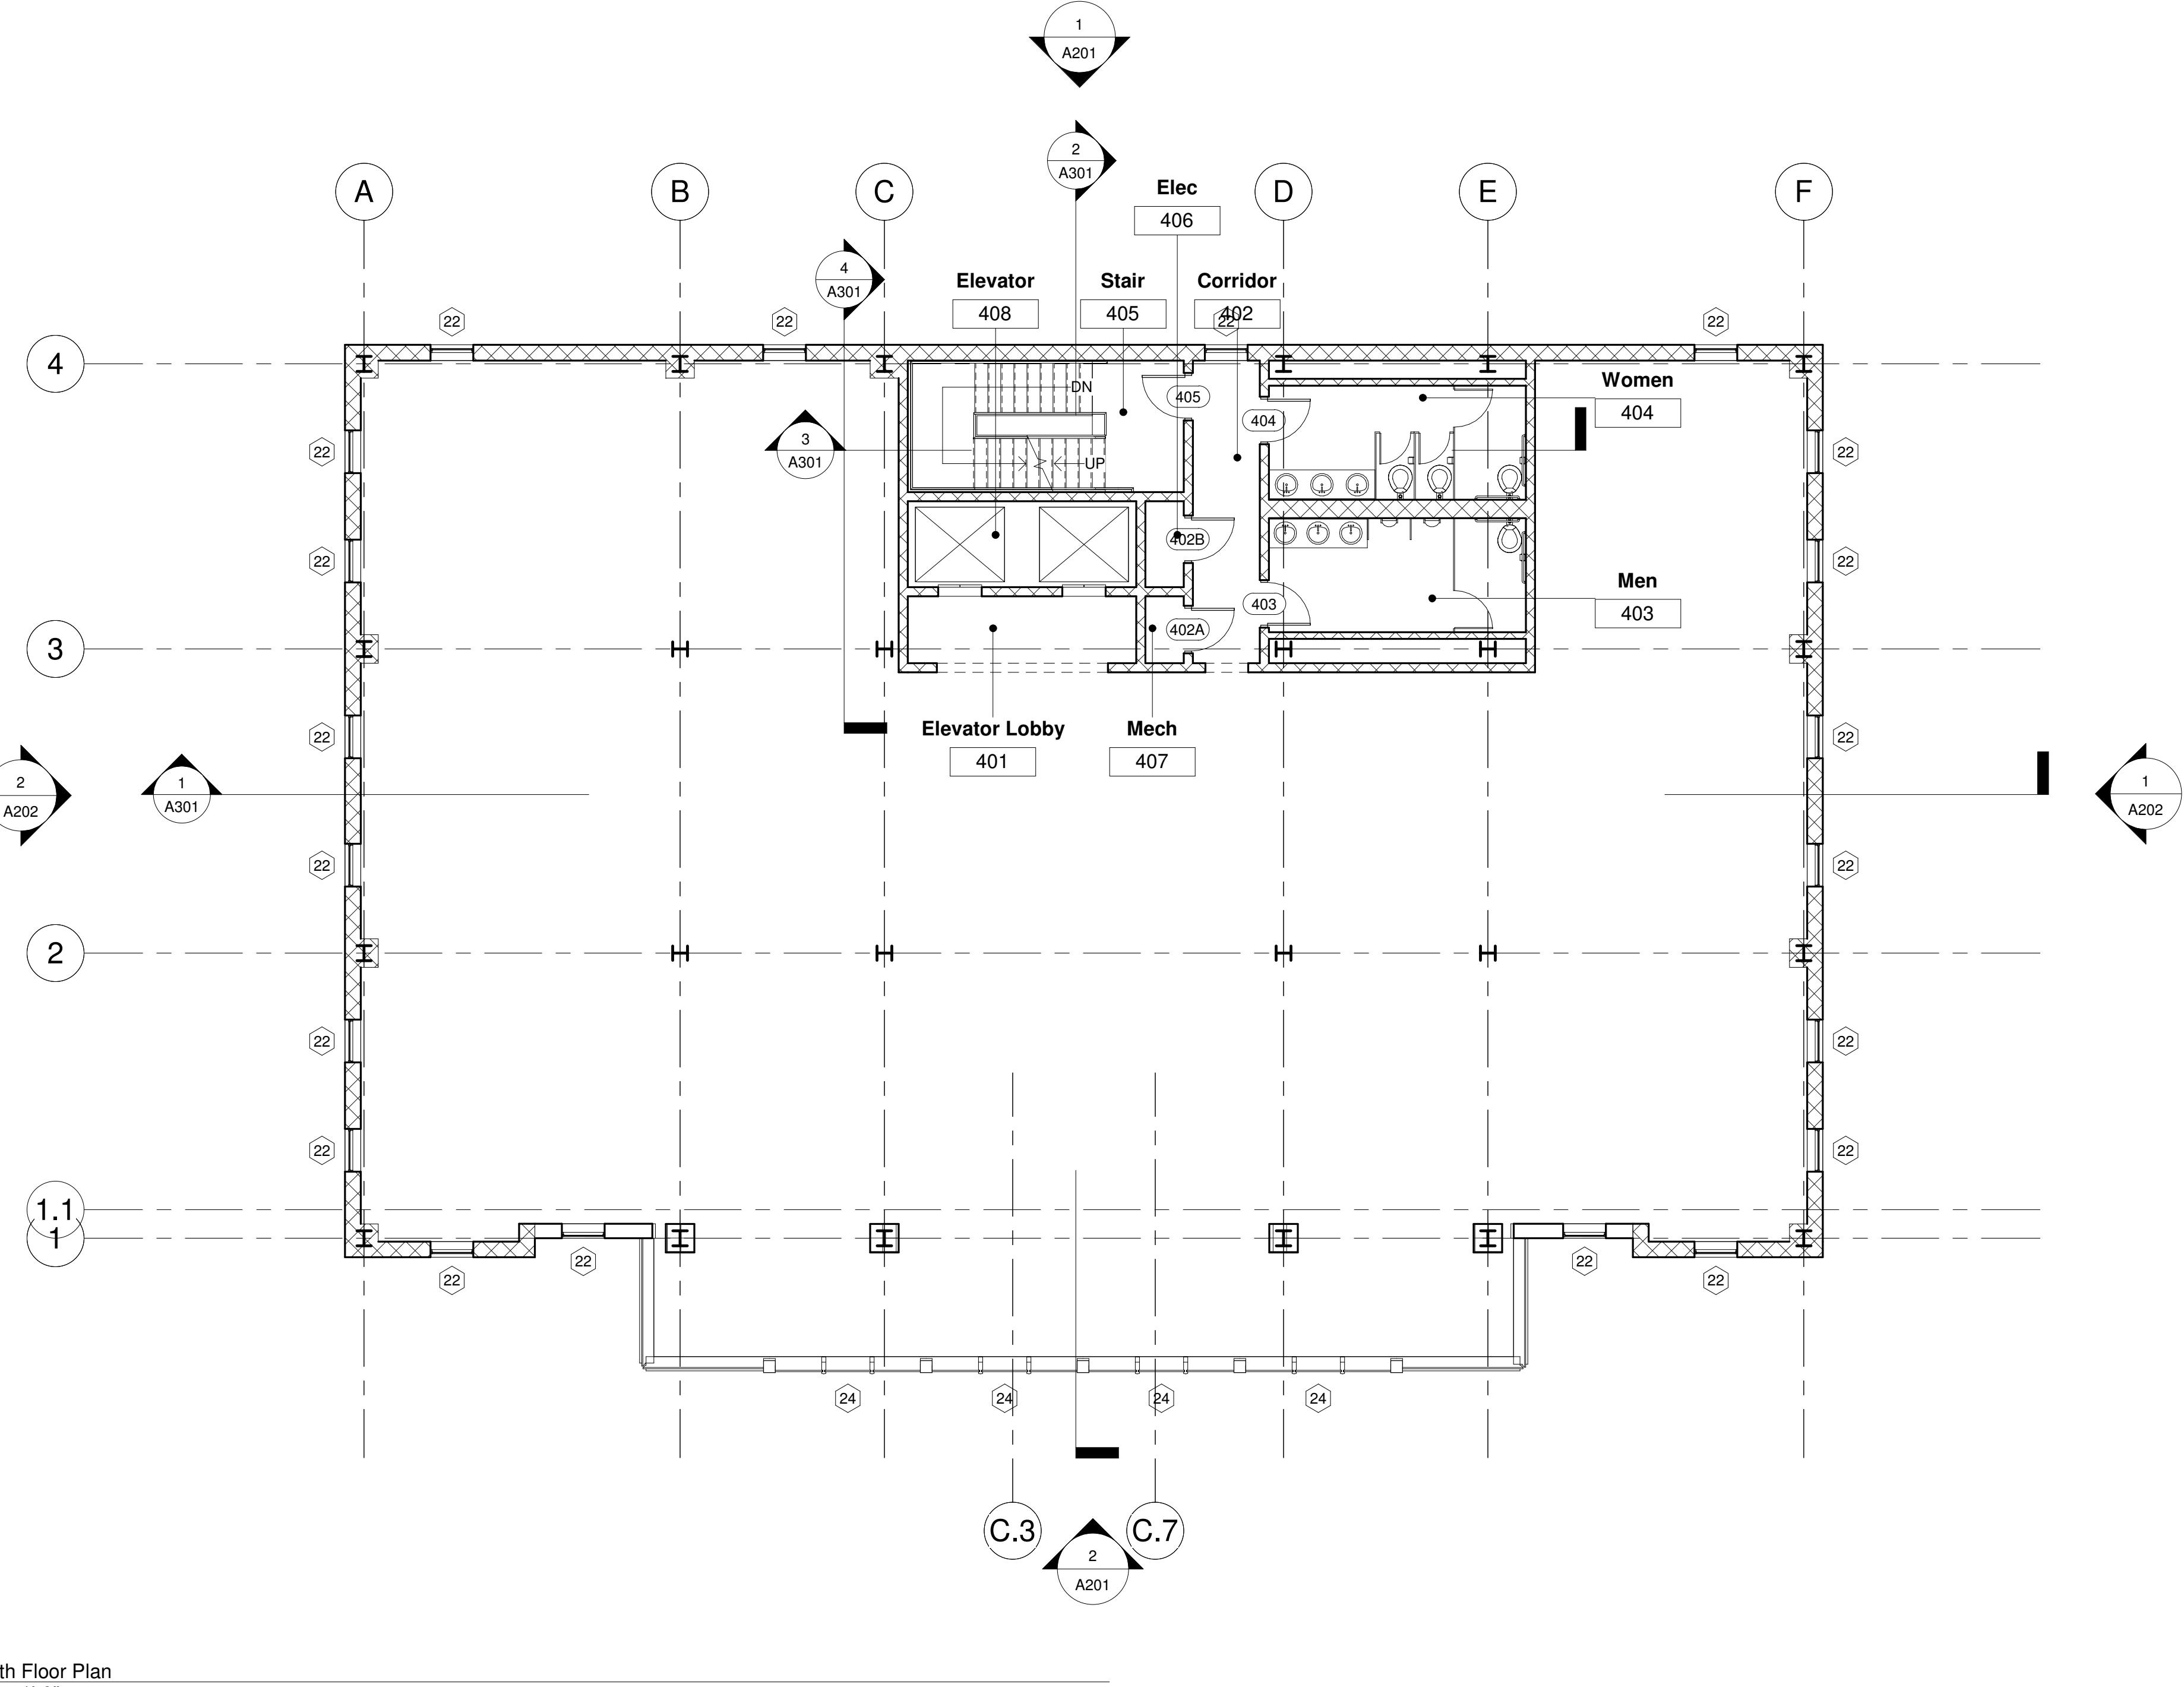

1 Fourth Floor Plan
1/8" = 1'-0"

PAUL F. AUBIN CONSULTING SERVICES

www.paulaubin.com

www.autodesk.com/revit

Consultant
Address
Address
Address
Phone


Printing and Output

15 Commercial Floor Plans

Project Number	2020.01A
Date	8/1/2020
Drawn By	PFA
Checked By	DPM

A104

cale $1/8"$ = 1'-0"

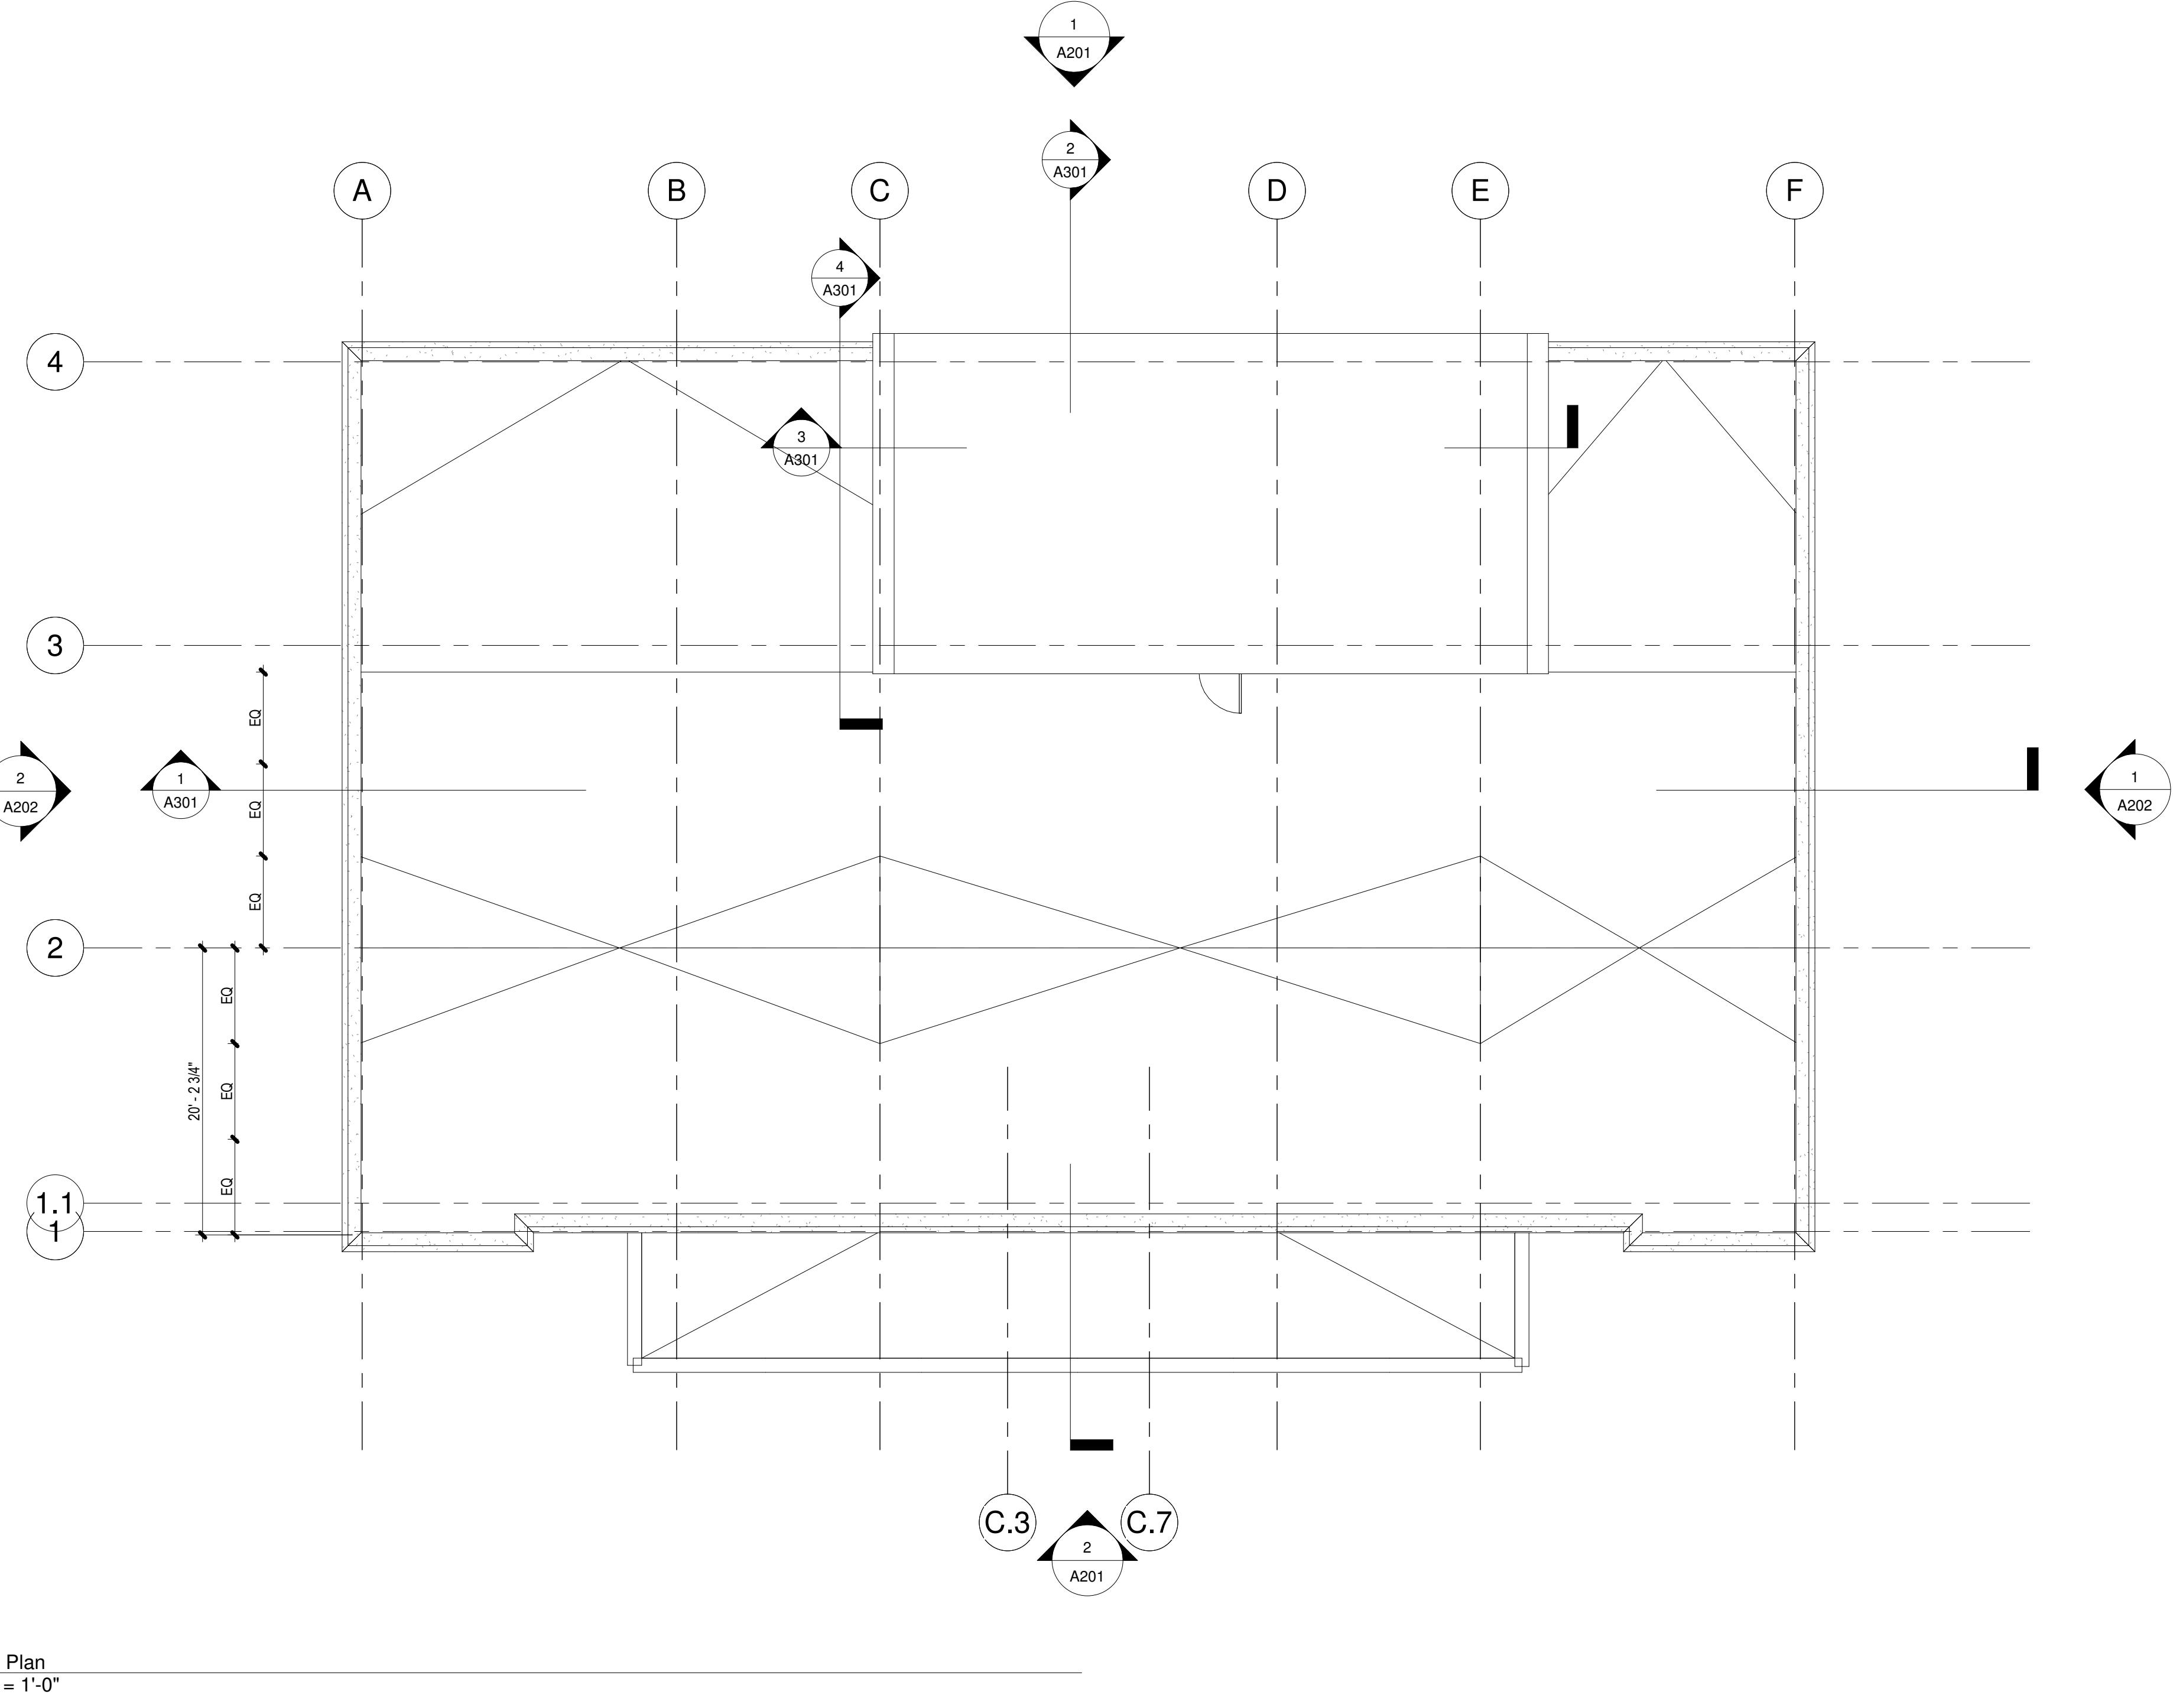


1 Roof Plan
1/8" = 1'-0"

Printing and Output

15 Commercial Roof Plan

Project Number	2020.01A
Date	8/1/2020
Drawn By	PFA
Checked By	DPM
A105	
Scale	1/8" = 1'-0"

Digitized by srujanika@gmail.com

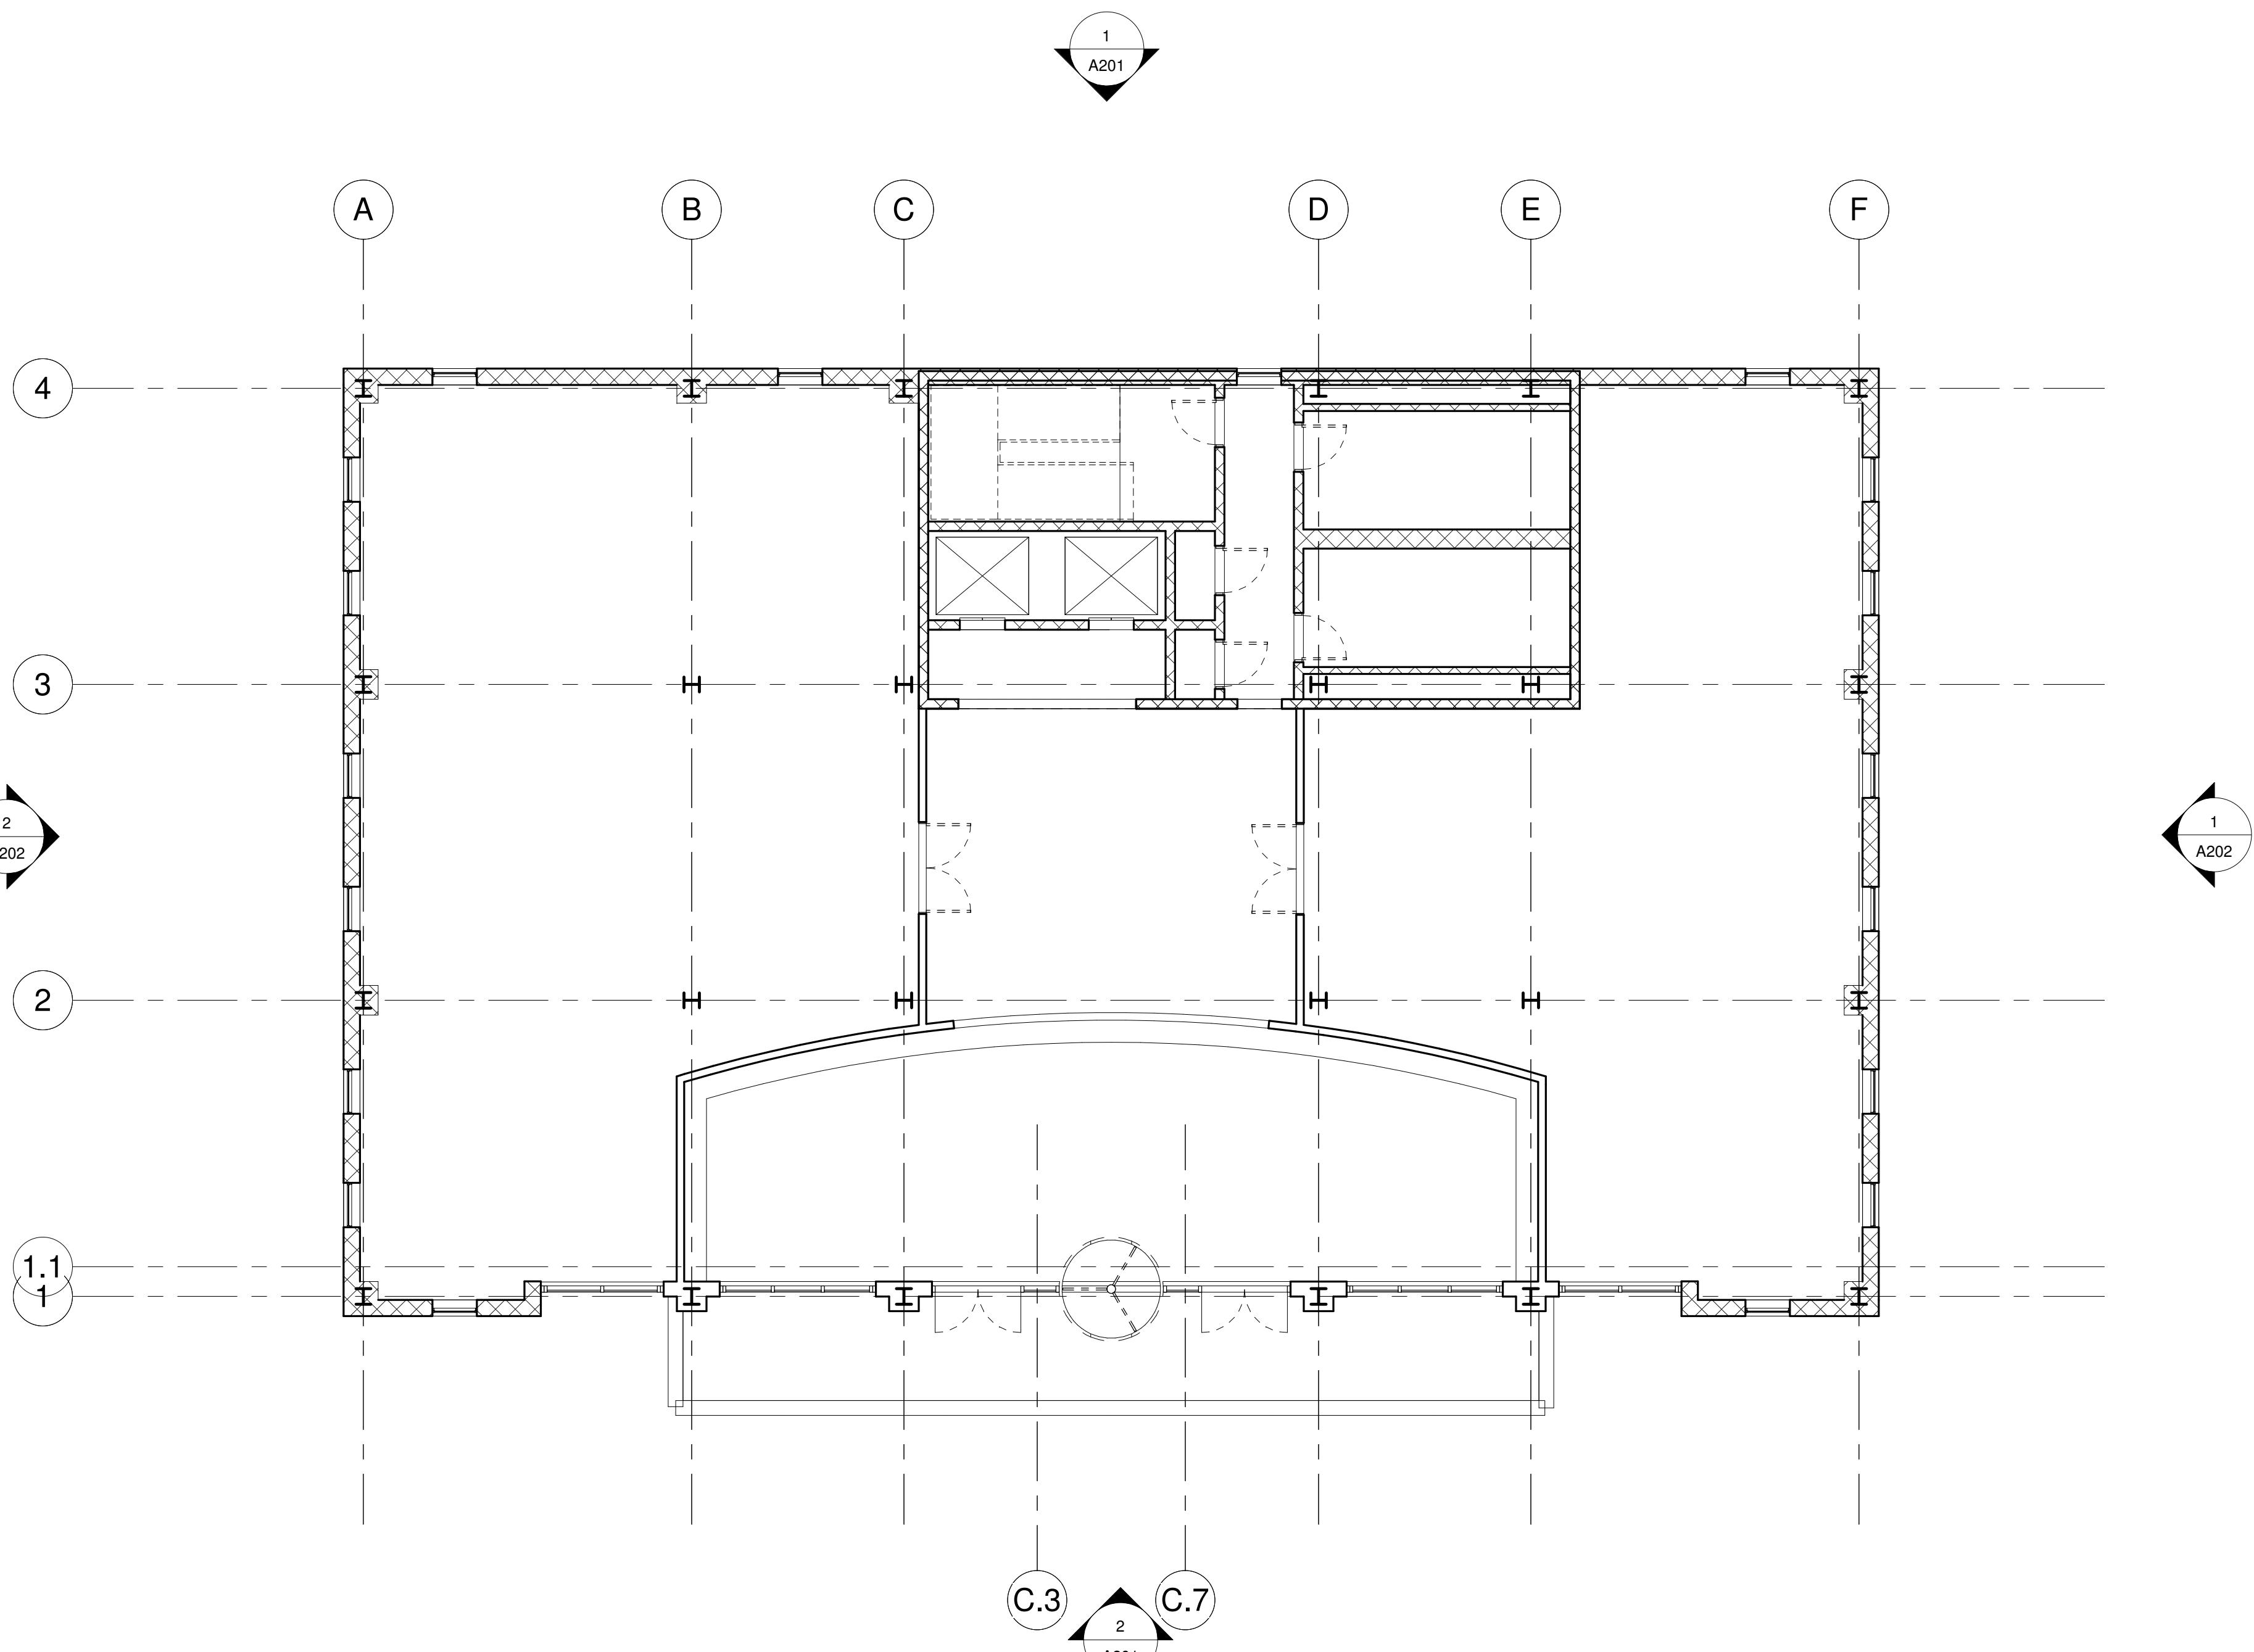

1 First Floor Reflected Ceiling Plan

PAUL F. AUBIN CONSULTING SERVICES

www.paulaubin.com

www.autodesk.com/revit

Consultant
Address
Address
Address
Phone


Printing and Output

15 Commercial Reflected Ceiling Plans

Project Number	2020.01A
Date	8/1/2020
Drawn By	PFA
Checked By	DPM
A111	
Scale	1/8" = 1'-0"

A 1 1 1

e **1/8" = 1'-0"**

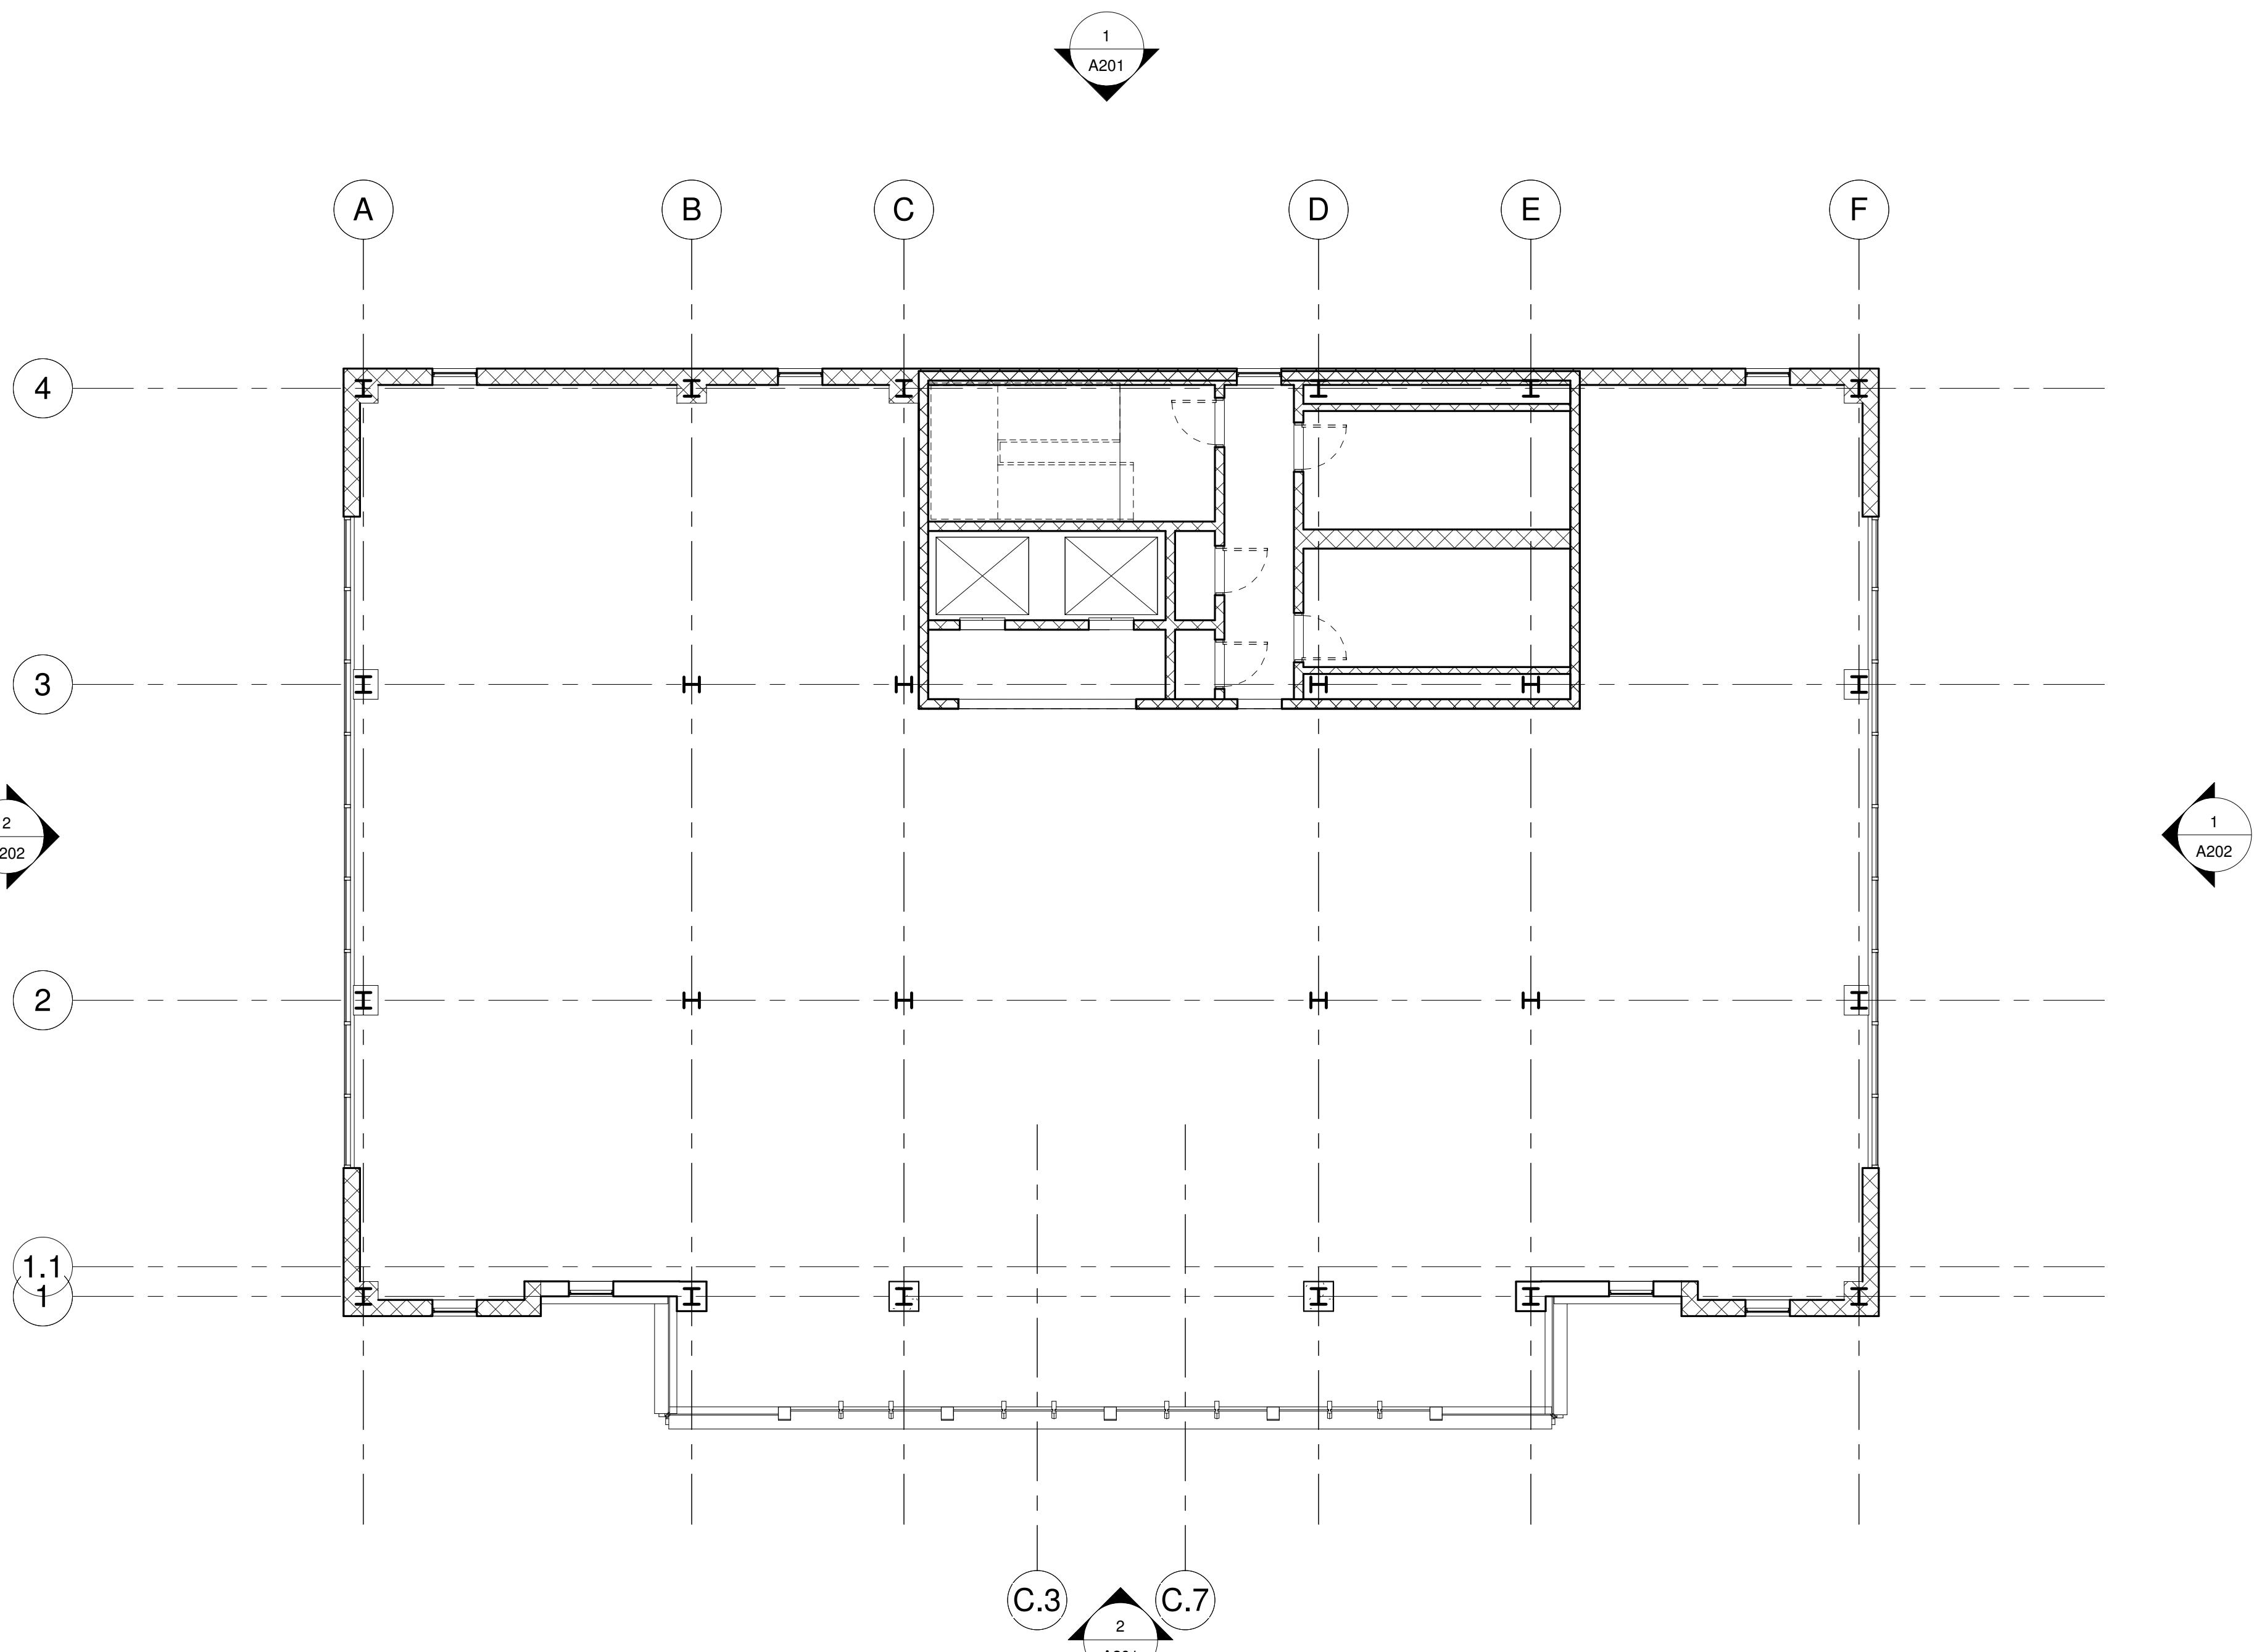


1 Second Floor Reflected Ceiling Plan
1/8" = 1'-0"

Printing and Output

15 Commercial Reflected Ceiling Plans

Project Number	2020.01A
Date	8/1/2020
Drawn By	PFA
Checked By	DPM
A112	
Scale	1/8" = 1'-0"

[View Details](#) | [Edit](#) | [Delete](#)

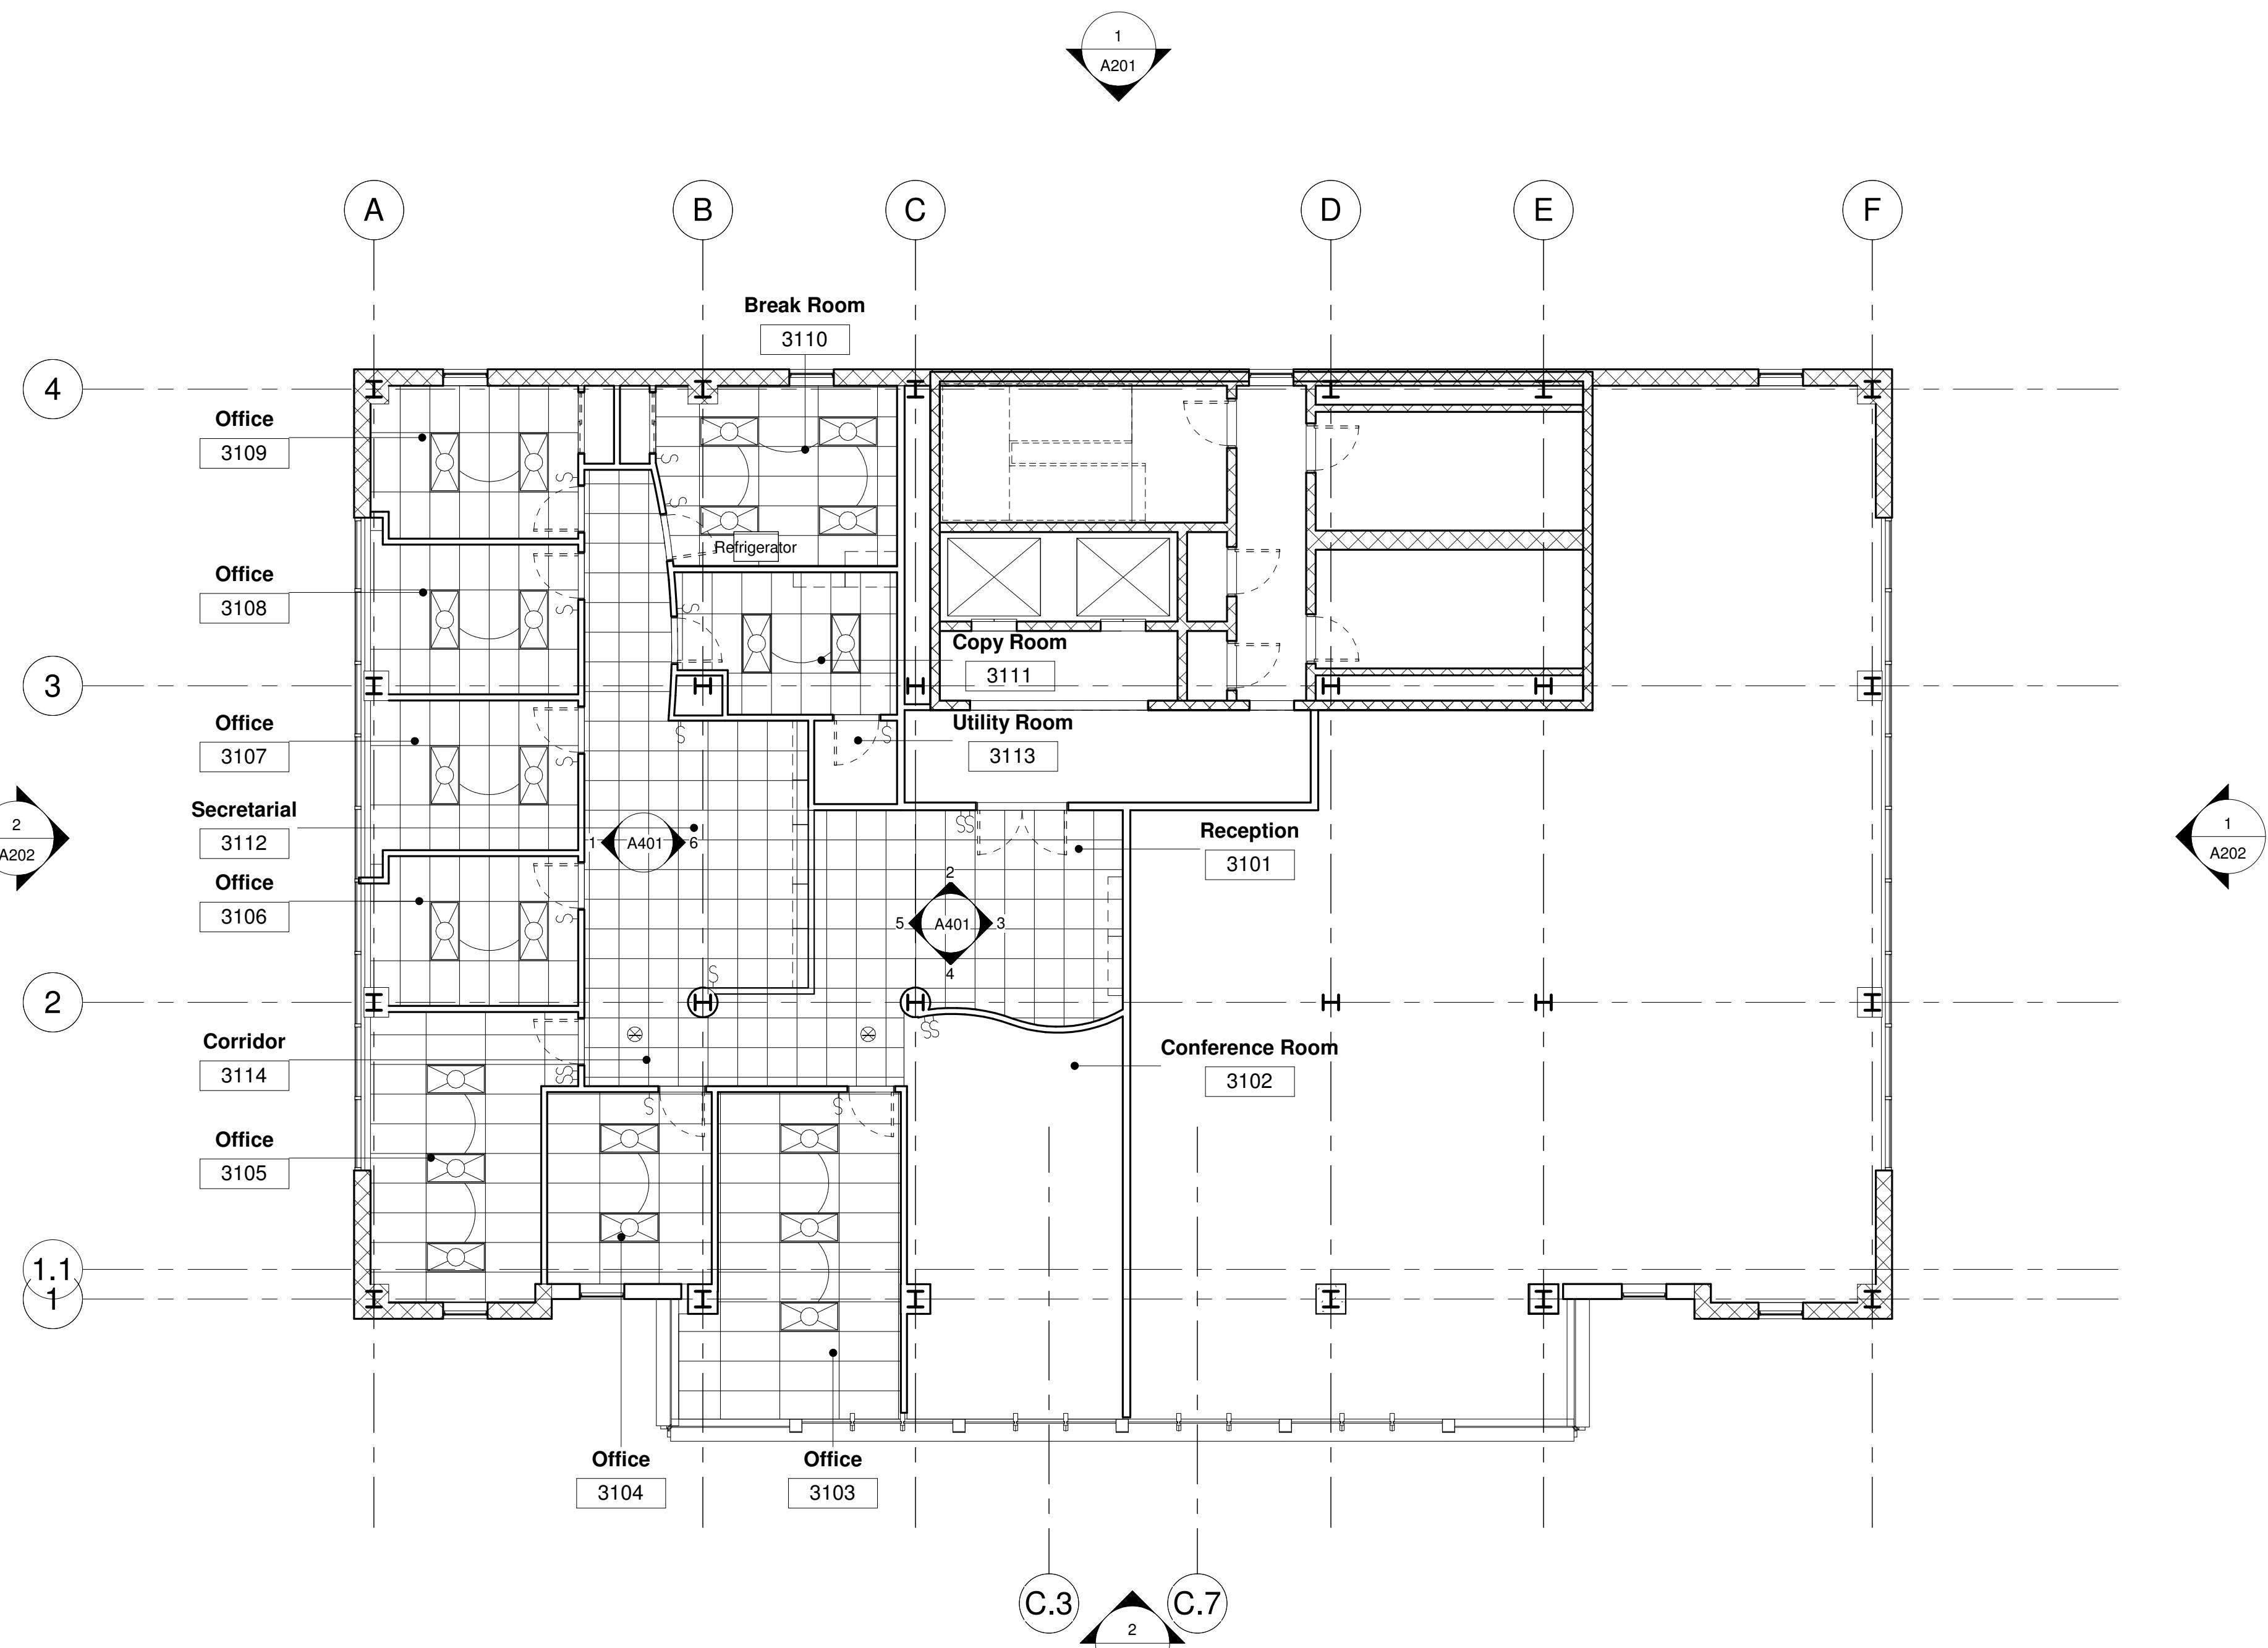


1 Third Floor Reflected Ceiling Plan
1/8" = 1'-0"

Printing and Output

15 Commercial Reflected Ceiling Plans

Project Number	2020.01A
Date	8/1/2020
Drawn By	PFA
Checked By	DPM
A113	
Scale	1/8" = 1'-0"

For more information about the study, please contact Dr. [REDACTED] at [REDACTED].

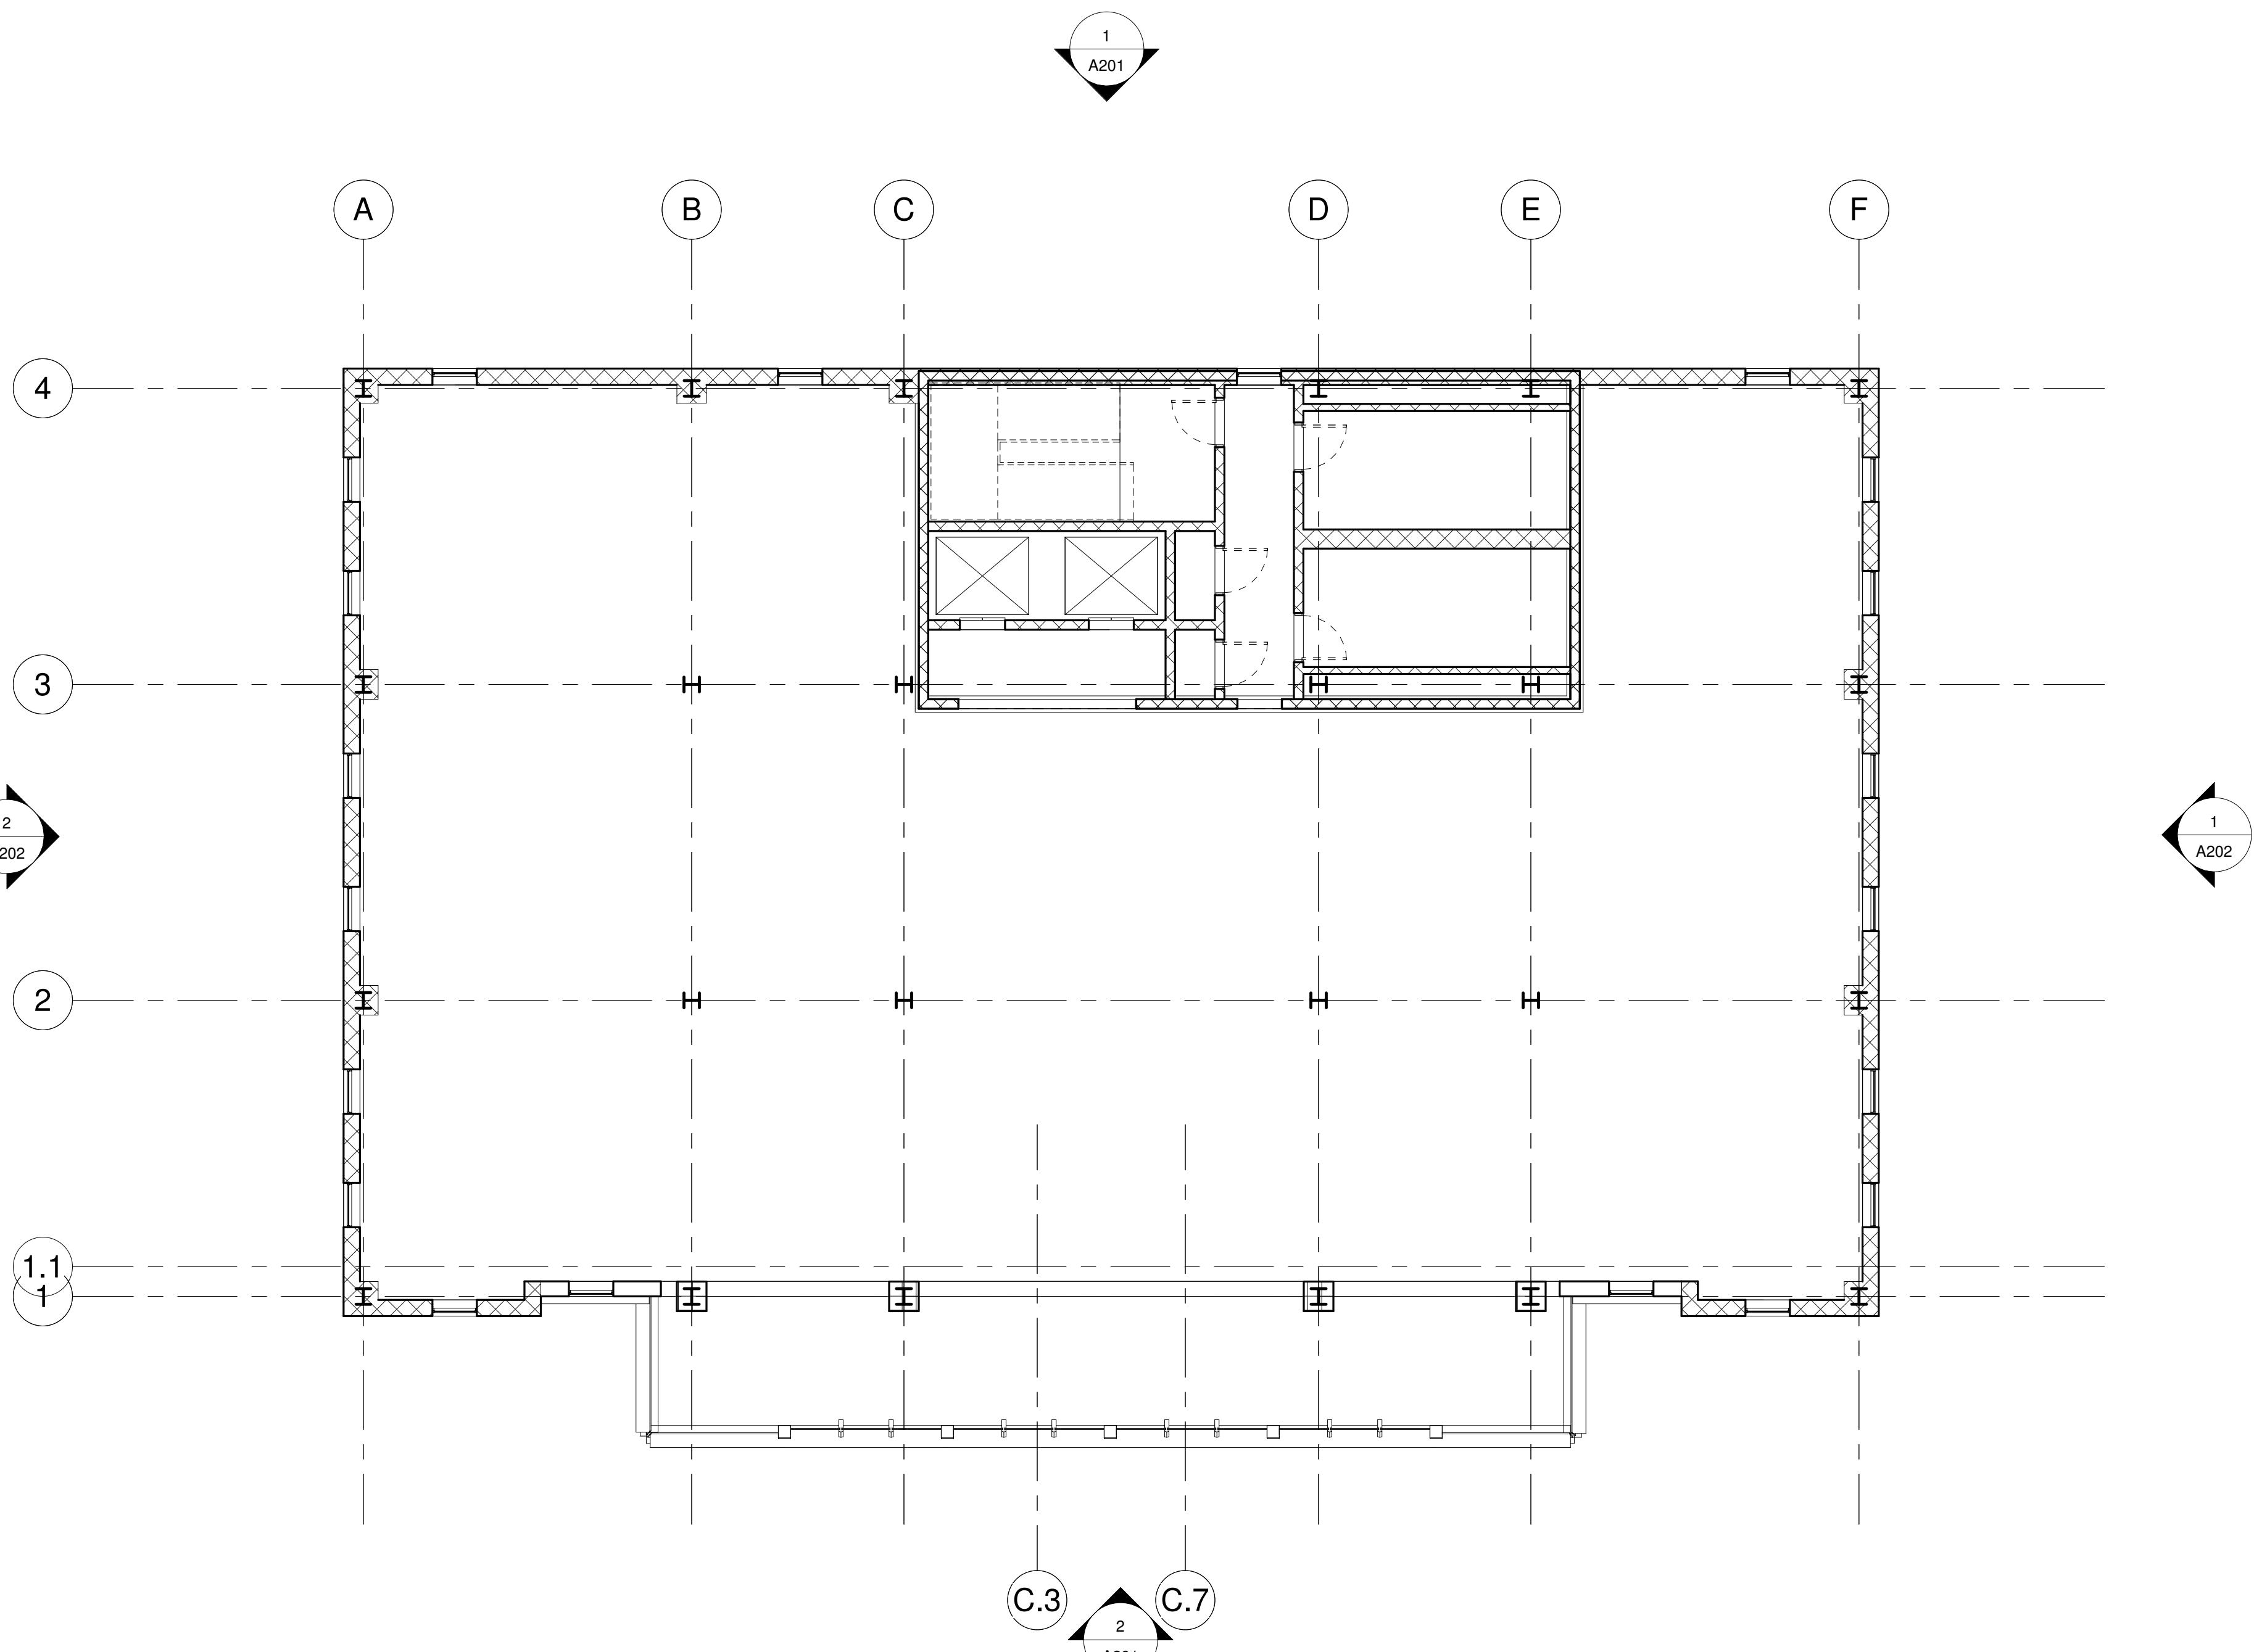


1 Fourth Floor Reflected Ceiling Plan
1/8" = 1'-0"

Printing and Output

15 Commercial Reflected Ceiling Plans

Project Number	2020.01A
Date	8/1/2020
Drawn By	PFA
Checked By	DPM
A114	
Scale	1/8" = 1'-0"

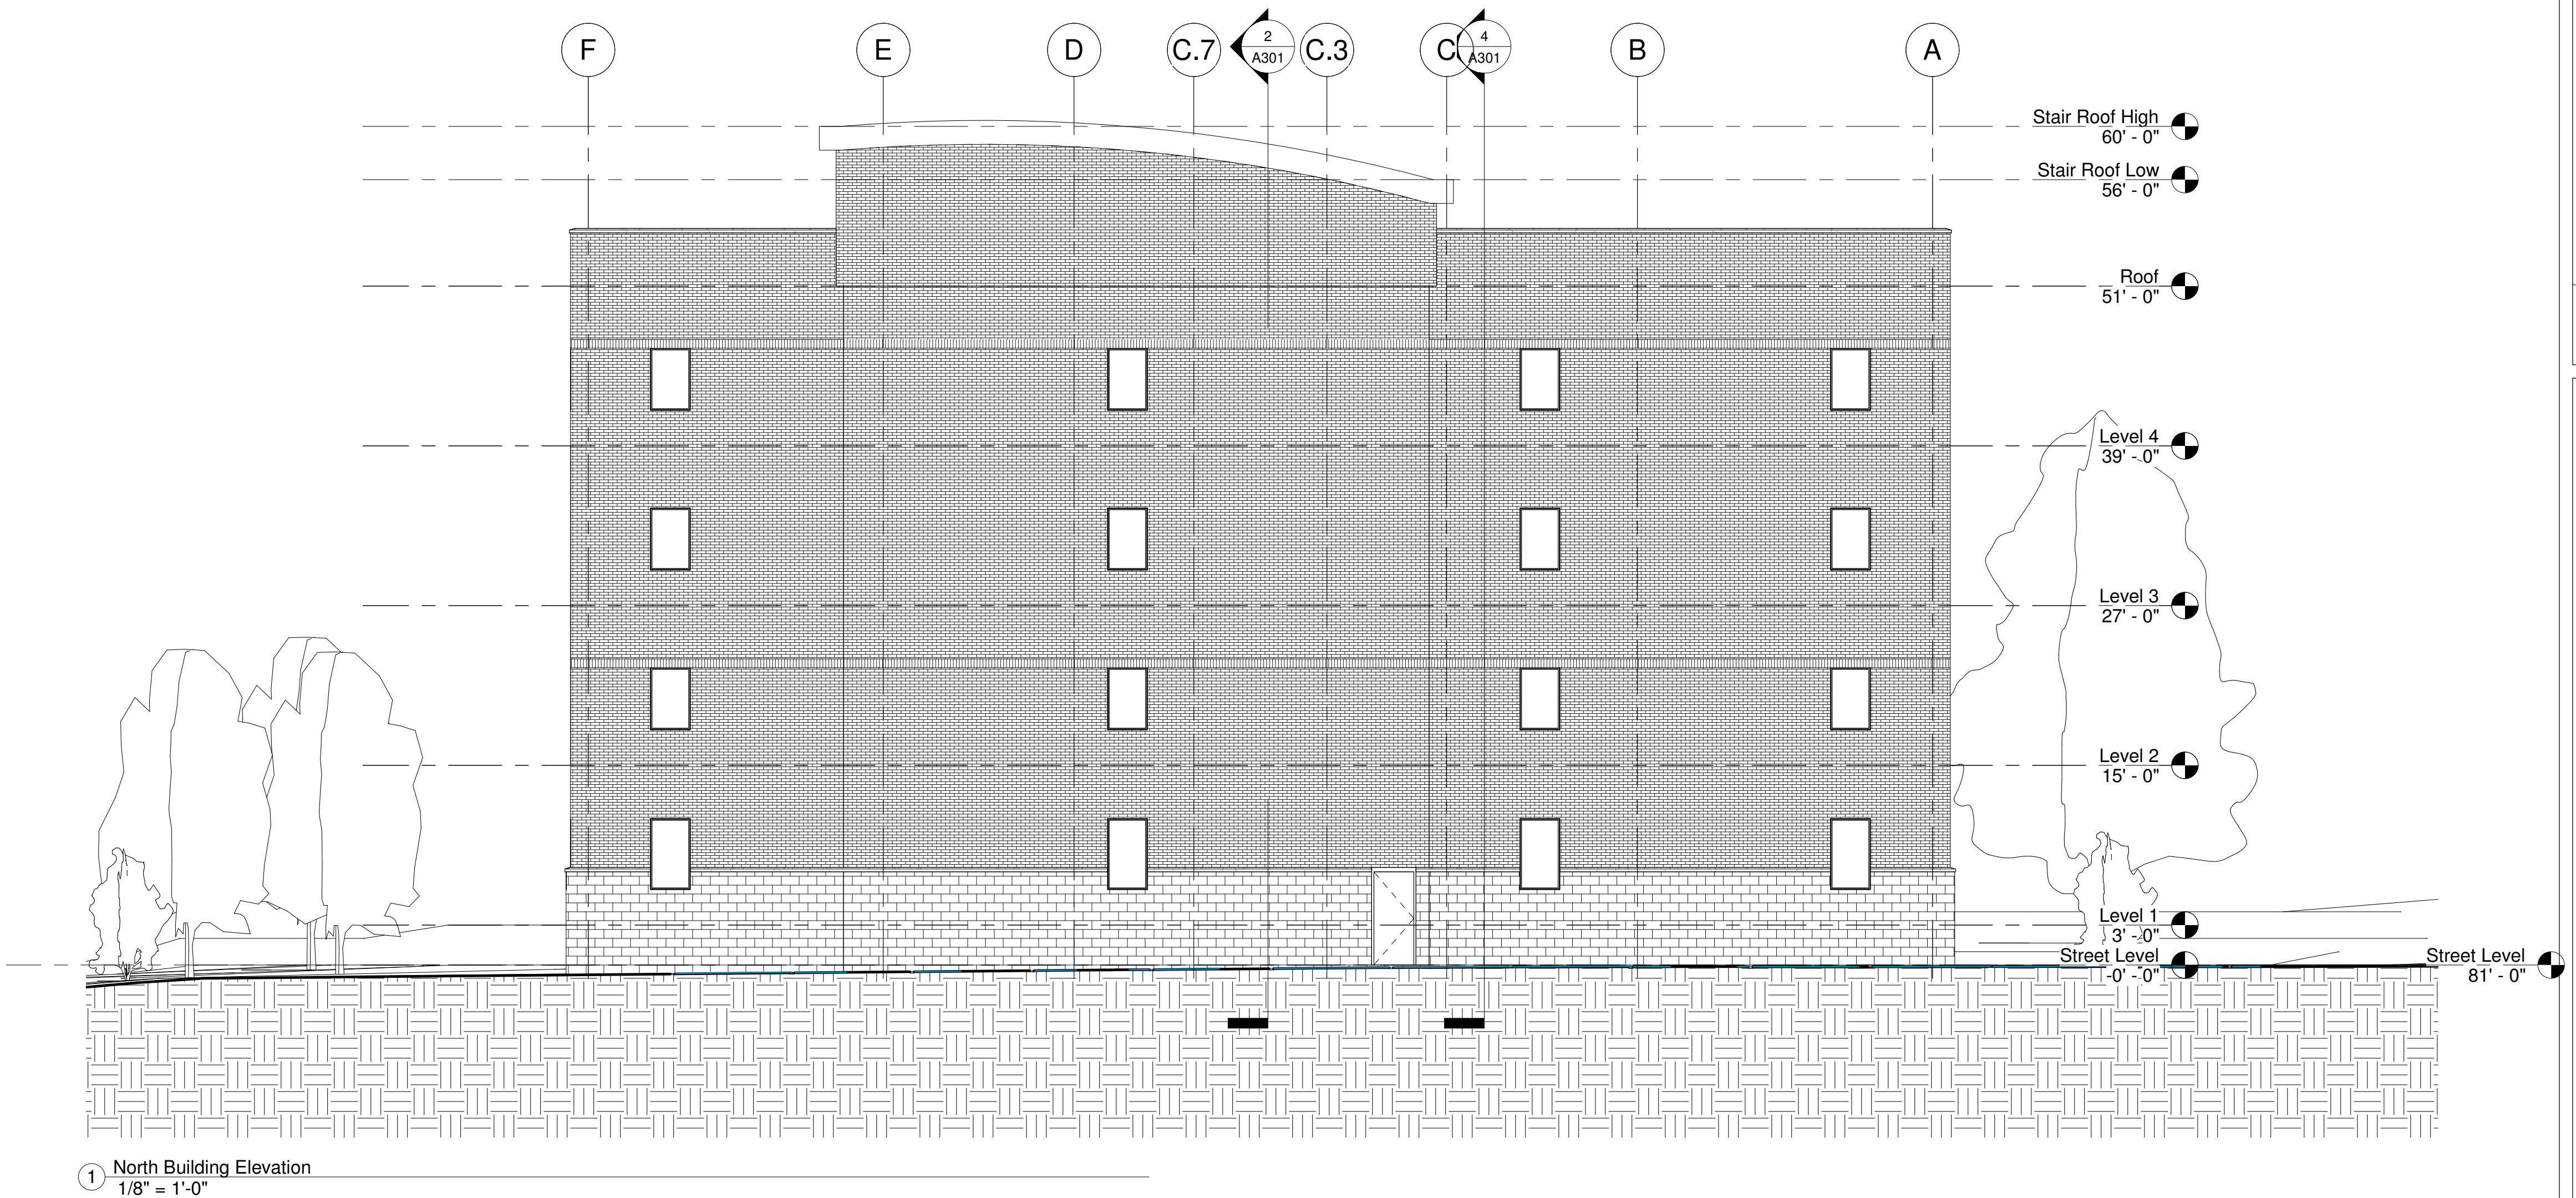

1 North Building Elevation
1/8" = 1'-0"



2 South Building Elevation
1/8" = 1'-0"

PAUL F. AUBIN
CONSULTING SERVICES

www.paulaubin.com

www.autodesk.com/revit

Consultant
Address
Address
Address
Phone

Printing and Output

15 Commercial Building Elevations

Project Number	2020.01A
Date	8/1/2020
Drawn By	PFA
Checked By	DPM


A201

Scale $1/8" = 1'-0"$



www.paulaubin.com

www.autodesk.com/revit

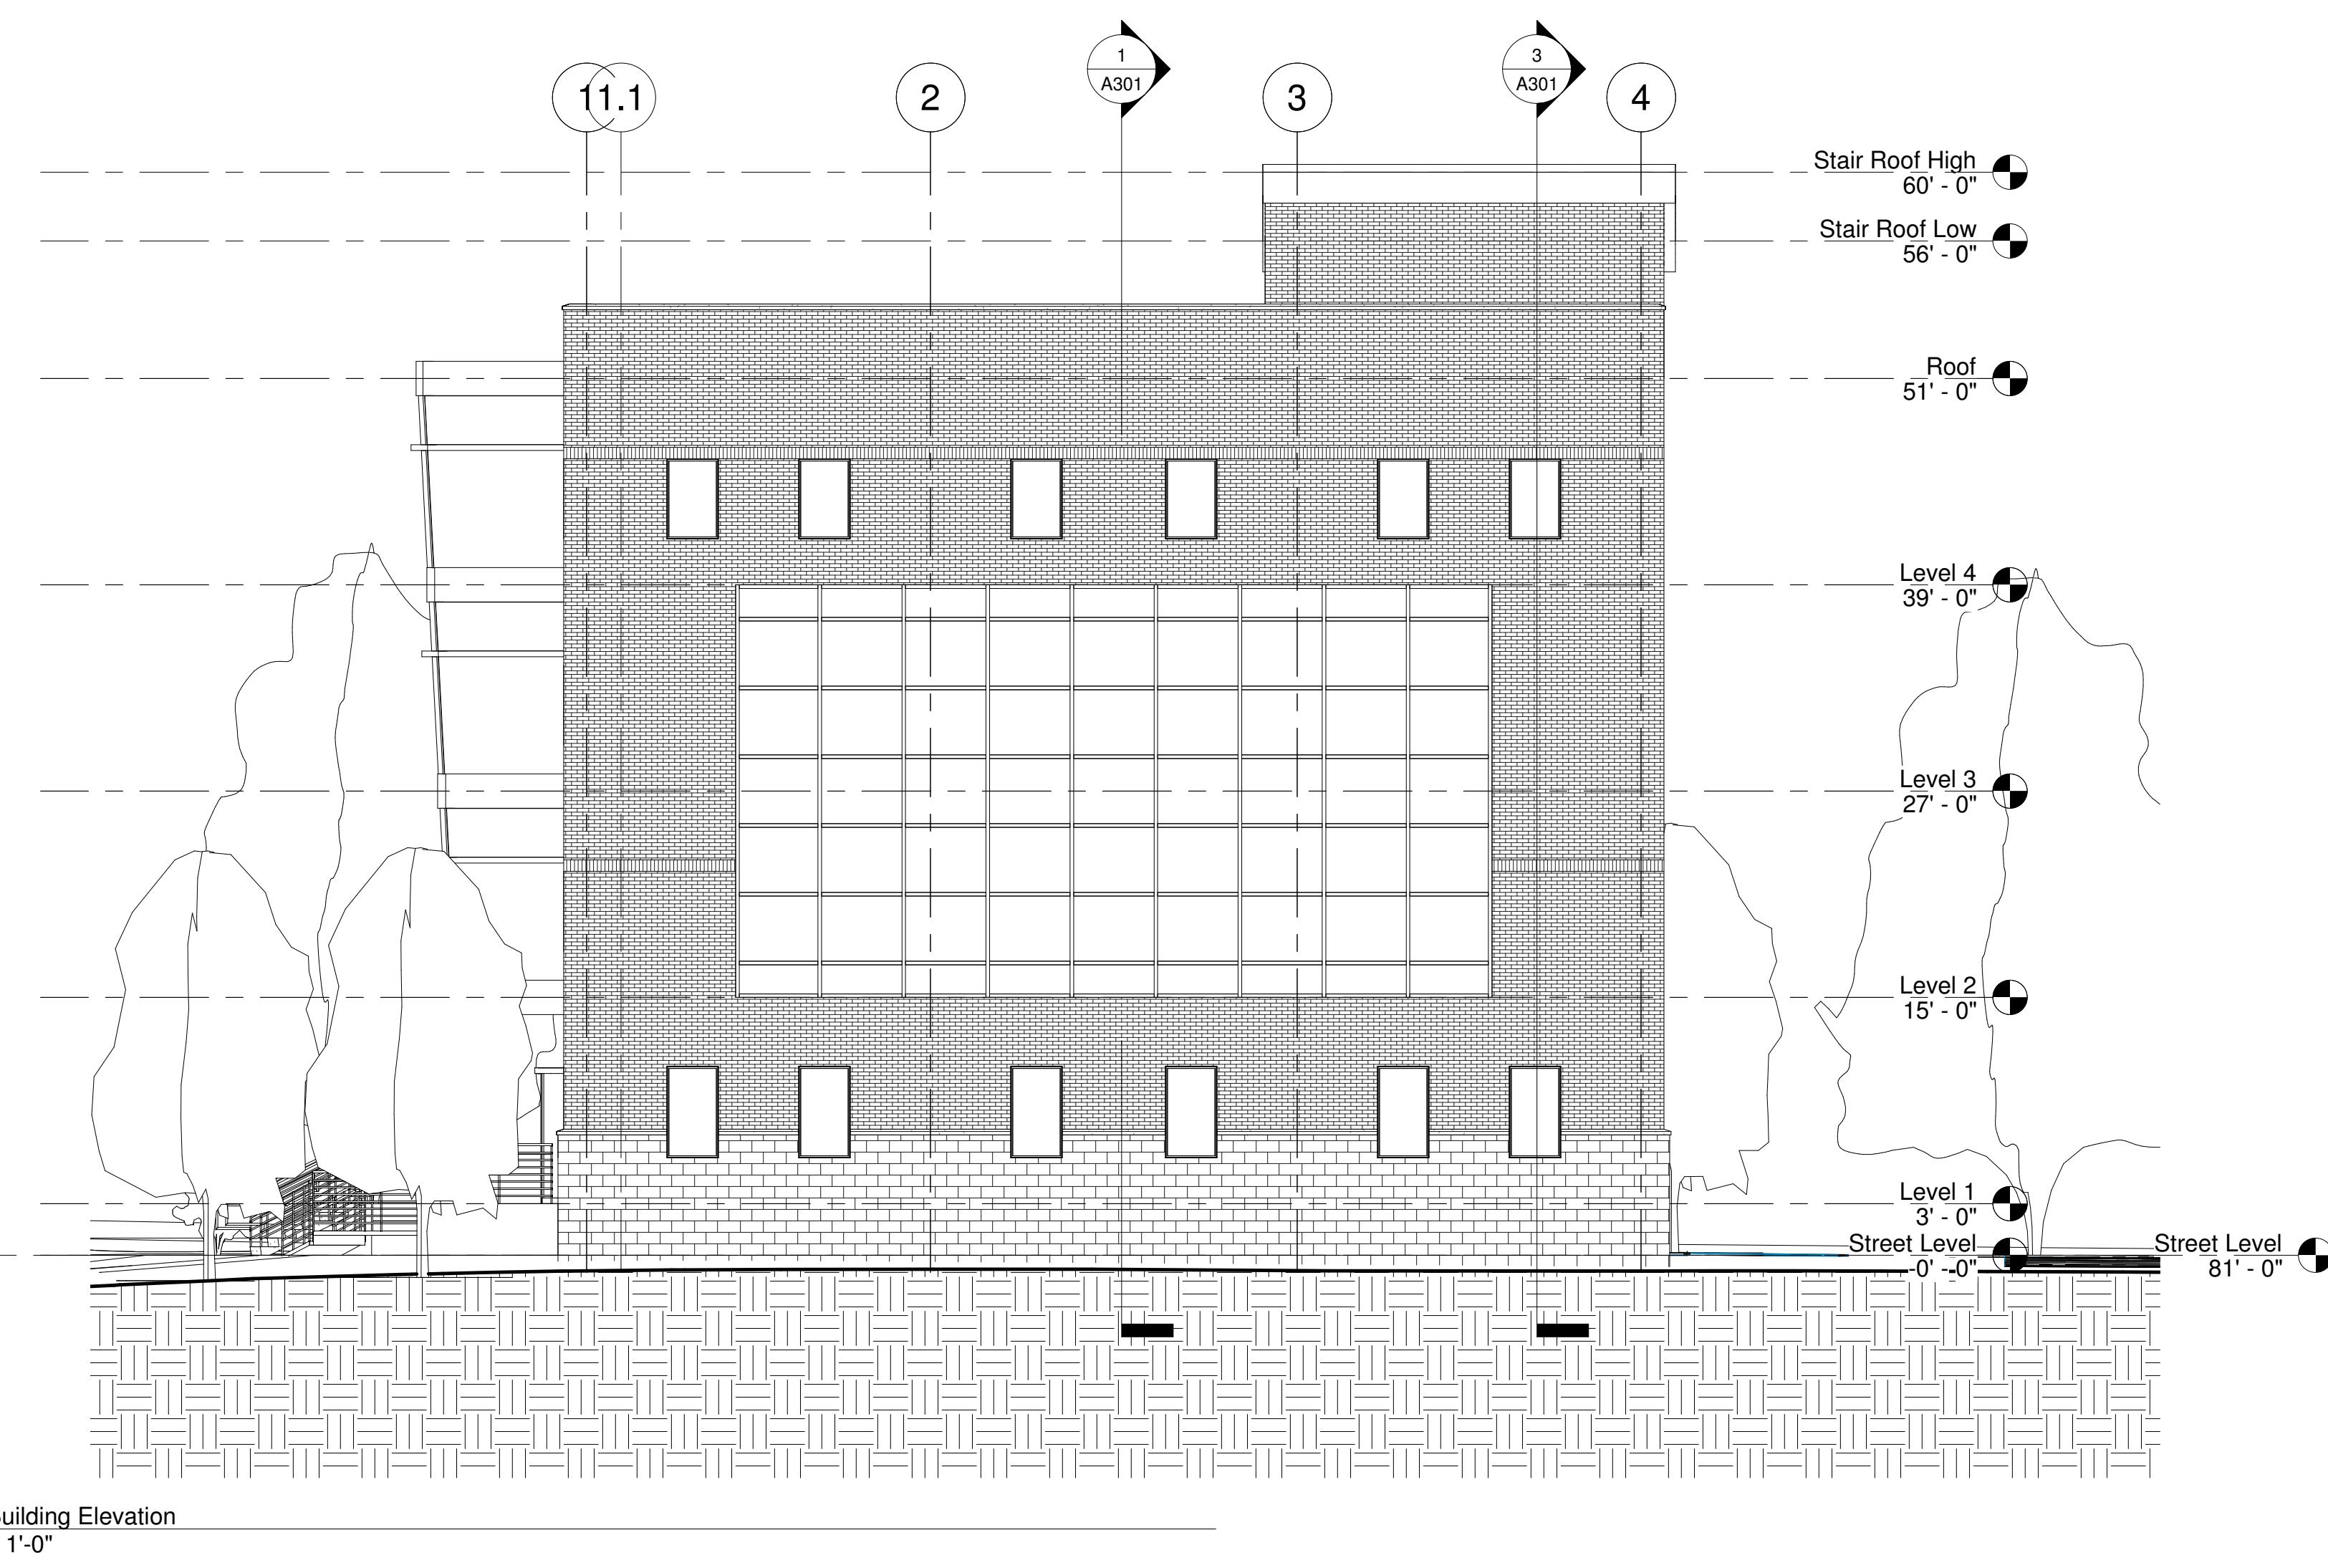

1 East Building Elevation



2 West Building Elevation
1/8" = 1'-0"


Printing and Output

15 Commercial Building Elevations

Project Number	2020.01A
Date	8/1/2020
Drawn By	PFA
Checked By	DPM


A202

1/8" = 1'-0"

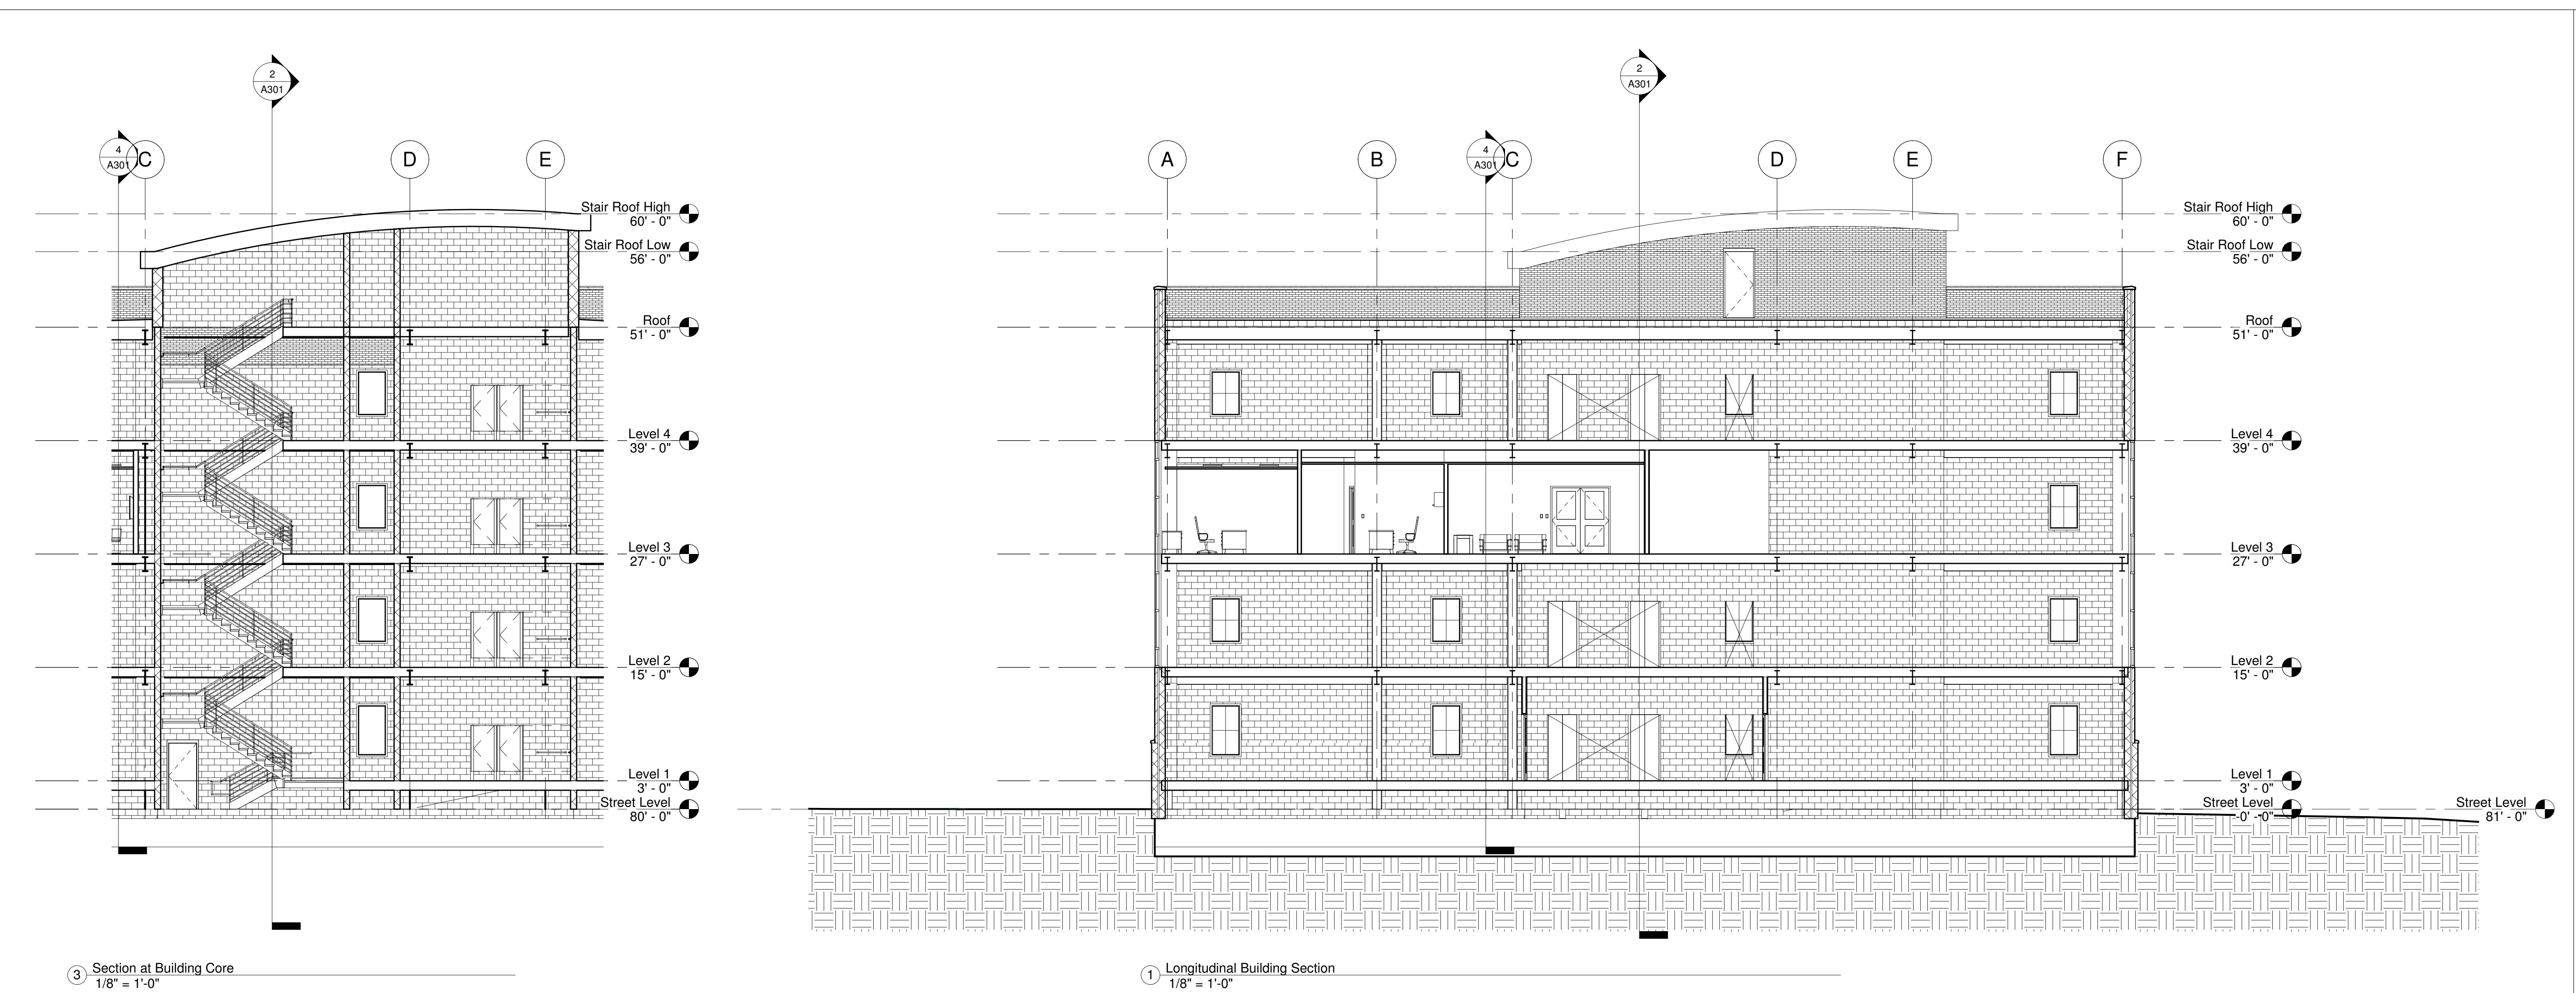

3 Section at Building Core
 $1/8" = 1'-0"$

1 Longitudinal Building Section
1/8" = 1'-0"

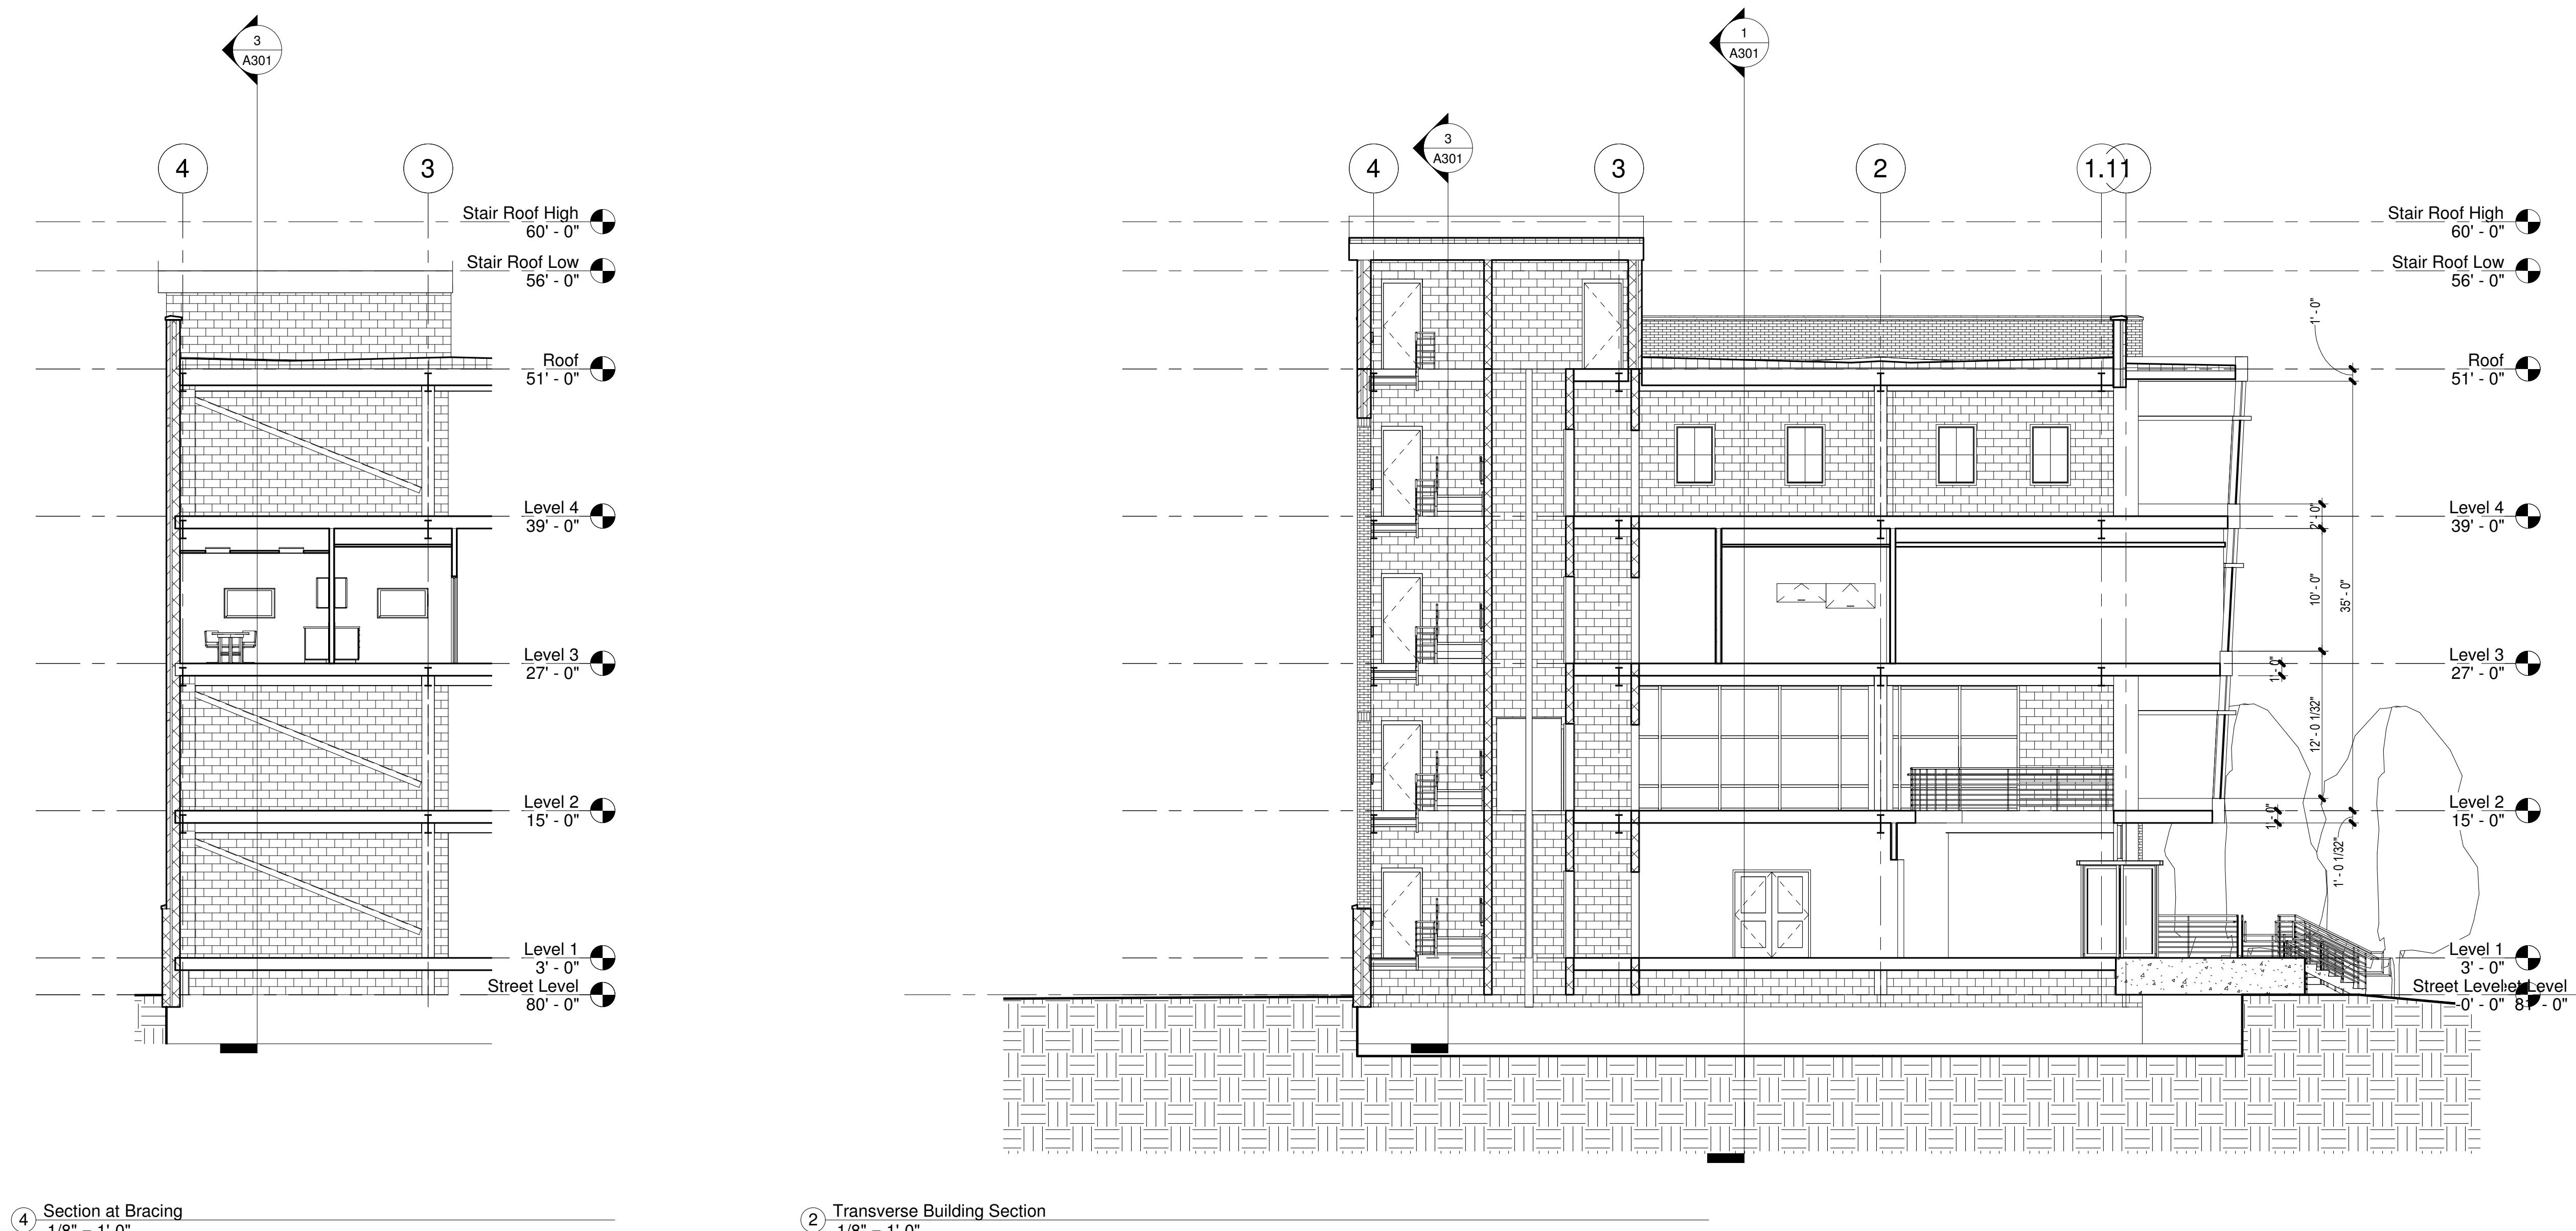

4 Section at Bracing
 $1/8" = 1'-0"$

2 Transverse Building Section

Printing and Output

15 Commercial Building Sections

Project Number	2020.01A
Date	8/1/2020
Drawn By	PFA
Checked By	DPM

A301

Scale **1/8" = 1'-0"**





PAUL F. AUBIN
CONSULTING SERVICES

www.paulaubin.com

www.autodesk.com/revit

Consultant
Address
Address
Address
Phone

Printing and Output

15 Commercial Interior Elevations

Object Number	2020.01A
Date	8/1/2020
Drawn By	Author
Checked By	Checker
A401	
Scale	1/2" = 1'-0"


Mark	Type	Door Schedule								Frame Schedule						Comments	
		Door				Frame				Type		Material		Finish			
Width	Height	Thickness	Material	Finish	Under Cut	Fire Rating	Hardware	Type	Material	Finish	Comments	Jamb	Head				
Street Level																	
100	1	3' - 0"	7' - 0"	0' - 1 3/4"	STL	Paint				A1	HM	Primed	1/A501	2/A501			
Level 1																	
102A	1	3' - 0"	7' - 0"	0' - 1 3/4"	STL	Paint				A1	HM	Primed	1/A501	2/A501			
102B	1	3' - 0"	7' - 0"	0' - 1 3/4"	STL	Paint				A1	HM	Primed	1/A501	2/A501			
103	1	3' - 0"	7' - 0"	0' - 1 3/4"	STL	Paint				A1	HM	Primed	1/A501	2/A501			
104	1	3' - 0"	7' - 0"	0' - 1 3/4"	STL	Paint				A1	HM	Primed	1/A501	2/A501			
105	1	3' - 0"	7' - 0"	0' - 1 3/4"	STL	Paint				A1	HM	Primed	1/A501	2/A501			
1001A	19	7' - 0"	7' - 10 1/2"							A1	HM	Primed	1/A501	2/A501			
1001B	17	5' - 9 1/2"	7' - 10 3/4"														
1001C	17	5' - 9 1/2"	7' - 10 3/4"														
1002A	20	6' - 0"	7' - 0"	0' - 1 3/4"													
1002B	20	6' - 0"	7' - 0"	0' - 1 3/4"													
Level 2																	
202A	1	3' - 0"	7' - 0"	0' - 1 3/4"	STL	Paint				A1	HM	Primed	1/A501	2/A501			
202B	1	3' - 0"	7' - 0"	0' - 1 3/4"	STL	Paint				A1	HM	Primed	1/A501	2/A501			
203	1	3' - 0"	7' - 0"	0' - 1 3/4"	STL	Paint				A1	HM	Primed	1/A501	2/A501			
204	1	3' - 0"	7' - 0"	0' - 1 3/4"	STL	Paint				A1	HM	Primed	1/A501	2/A501			
205	1	3' - 0"	7' - 0"	0' - 1 3/4"	STL	Paint				A1	HM	Primed	1/A501	2/A501			
Level 3																	
302A	1	3' - 0"	7' - 0"	0' - 1 3/4"	STL	Paint				A1	HM	Primed	1/A501	2/A501			
302B	1	3' - 0"	7' - 0"	0' - 1 3/4"	STL	Paint				A1	HM	Primed	1/A501	2/A501			
303	1	3' - 0"	7' - 0"	0' - 1 3/4"	STL	Paint				A1	HM	Primed	1/A501	2/A501			
304	1	3' - 0"	7' - 0"	0' - 1 3/4"	STL	Paint				A1	HM	Primed	1/A501	2/A501			
305	1	3' - 0"	7' - 0"	0' - 1 3/4"	STL	Paint				A1	HM	Primed	1/A501	2/A501			
3101	20	6' - 0"	7' - 0"	0' - 1 3/4"													
3103	32	3' - 0"	7' - 0"	0' - 1 3/4"													
3104	32	3' - 0"	7' - 0"	0' - 1 3/4"													
3105	32	3' - 0"	7' - 0"	0' - 1 3/4"													
3106	32	3' - 0"	7' - 0"	0' - 1 3/4"													
3108	32	3' - 0"	7' - 0"	0' - 1 3/4"													
3109A	32	3' - 0"	7' - 0"	0' - 1 3/4"													
3109B	21	4' - 0"	7' - 0"	0' - 1 3/8"													
3110A	32	3' - 0"	7' - 0"	0' - 1 3/4"													
3110B	21	4' - 0"	7' - 0"	0' - 1 3/8"													
3111	32	3' - 0"	7' - 0"	0' - 1 3/4"													
3113	1	3' - 0"	7' - 0"	0' - 1 3/4"	STL	Paint				A1	HM	Primed	1/A501	2/A501			
3114	32	3' - 0"	7' - 0"	0' - 1 3/4"													
Level 4																	
402A	1	3' - 0"	7' - 0"	0' - 1 3/4"	STL	Paint				A1	HM	Primed	1/A501	2/A501			
402B	1	3' - 0"	7' - 0"	0' - 1 3/4"	STL	Paint				A1	HM	Primed	1/A501	2/A501			
403	1	3' - 0"	7' - 0"	0' - 1 3/4"	STL	Paint				A1	HM	Primed	1/A501	2/A501			
404	1	3' - 0"	7' - 0"	0' - 1 3/4"	STL	Paint				A1	HM	Primed	1/A501	2/A501			
405	1	3' - 0"	7' - 0"	0' - 1 3/4"	STL	Paint				A1	HM	Primed	1/A501	2/A501			
Roof																	
502A	1	3' - 0"	7' - 0"	0' - 1 3/4"	STL	Paint				A1	HM	Primed	1/A501	2/A501			
502B	1	3' - 0"	7' - 0"	0' - 1 3/4"	STL	Paint				A1	HM	Primed	1/A501	2/A501			
503	1	3' - 0"	7' - 0"	0' - 1 3/4"	STL	Paint				A1	HM	Primed	1/A501	2/A501			
505	1	3' - 0"	7' - 0"	0' - 1 3/4"	STL	Paint				A1	HM	Primed	1/A501	2/A501			
508	1	3' - 0"	7' - 0"	0' - 1 3/4"	STL	Paint				A1	HM	Primed	1/A501	2/A501			

Room Schedule							
Room Number	Room Name	Floor Finish	Base Finish	Wall Finish	Ceiling Finish	Ceiling Height	Comments
101	Elevator Lobby						
102	Corridor						
103	Men						
104	Women						
105	Stair						
106	Elec						
107	Mech						
108	Elevator						
1001	Main Lobby						
1002	Level 1 Foyer						

Furniture Schedule						
Type Mark	Model	Cost	Count	Comments	Type	Image
Acme Furniture						
CH-1	ExecuChair	\$8,750.00	10			
DK-1	MAN-1234	\$3,600.00	3			
DK-2	TSK-5679	\$4,200.00	4			
TB-1	TBL3456	\$1,875.00	5			
TB-2	TBL-12CH	\$9,250.00	1			
TB-3	TBL-2424	\$1,250.00	1			

Acme Furniture: 24 \$28,925.00

Corporate Concepts

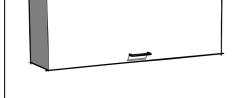BN-1	BIN-3618	\$1,250.00	2		
BN-2	BIN-4818	\$2,700.00	4		
BN-3	BIN-4824	\$785.00	1		
TV-1	TV50	\$900.00	2		

**Corporate
Concepts: 9** \$5,635.00

Fine Millwork, Inc.

DK-4	CUSTOM	\$2,750.00	1		
------	--------	------------	---	--	---



Fine Millwork, Inc.: 1 \$2,750.00

Furniture Concepts
CH 3 CHTSK 0

CH-3	CHTSK-095	\$2,190.00	2		
CH-4	CHTSK-895	\$8,950.00	10		
CR-1	CR-00998 877	\$11,720.00	8		
DK-3	SEC-4567	\$1,790.00	2	Include Keyboard Tray and Footrest Option	

Furniture Concepts: \$24,650.00

Office Systems

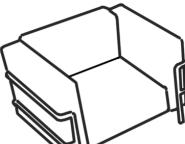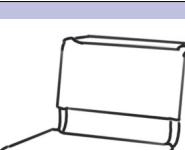Office Systems				
Product ID	Designer	Price	Stock Level	Image
CH-2	Corbu123	\$5,400.00	4	
CH-5	Breuer789	\$9,000.00	20	

Office Systems: 24 \$14,400.00

Total of all Furniture \$76,360.00

Items: 80



www.paulaubin.com

Consultant
Address
Address
Address
Phone

Printing and Output

15 Commercial Schedules

Project Number	2020.01A
Date	8/1/2020
Drawn By	Author
Checked By	Checker
Scale	A602

A602

Scale

Wall Schedule				
Type Mark	Length	Width	Family and Type	Comments
	8' - 0 9/16"		Curtain Wall: Front Façade	
	58' - 9 1/2"		Curtain Wall: Front Façade	
	8' - 0 9/16"		Curtain Wall: Front Façade	
B1	22' - 3 3/16"	0' - 7 5/8"	Basic Wall: REA 8" Masonry	
B1	44' - 0"	0' - 7 5/8"	Basic Wall: REA 8" Masonry	
B1	22' - 3 3/16"	0' - 7 5/8"	Basic Wall: REA 8" Masonry	
B1	22' - 1 3/16"	0' - 7 5/8"	Basic Wall: REA 8" Masonry	
B1	22' - 1 3/16"	0' - 7 5/8"	Basic Wall: REA 8" Masonry	
B1	20' - 0"	0' - 7 5/8"	Basic Wall: REA 8" Masonry	
B1	20' - 0"	0' - 7 5/8"	Basic Wall: REA 8" Masonry	
B1	12' - 0"	0' - 7 5/8"	Basic Wall: REA 8" Masonry	
	22' - 1 3/16"	1' - 1 1/4"	Basic Wall: Exterior Shell	
	44' - 0"	1' - 1 1/4"	Basic Wall: Exterior Shell	
	22' - 1 3/16"	1' - 1 1/4"	Basic Wall: Exterior Shell	
	44' - 0"	1' - 1 1/4"	Basic Wall: Exterior Shell	
B1	16' - 9 3/16"	0' - 7 5/8"	Basic Wall: REA 8" Masonry	
B1	22' - 1 3/16"	0' - 7 5/8"	Basic Wall: REA 8" Masonry	
B1	20' - 0"	0' - 7 5/8"	Basic Wall: REA 8" Masonry	
B1	3' - 4"	0' - 7 5/8"	Basic Wall: REA 8" Masonry	
B1	12' - 0"	0' - 7 5/8"	Basic Wall: REA 8" Masonry	
	77' - 0 11/32"		Curtain Wall: Curtain Wall 1	
	44' - 0"		Curtain Wall: Storefront - Levels 2 to 3	
	44' - 0"		Curtain Wall: Storefront - Levels 2 to 3	
	78' - 1 19/32"	1' - 0 1/4"	Basic Wall: Exterior - EIFS on Mtl. Stud	
	38' - 9 3/16"	1' - 5 1/4"	Basic Wall: Exterior Base	
	38' - 7 3/16"	1' - 1 1/4"	Basic Wall: Exterior Shell	
	38' - 7 3/16"	1' - 1 1/4"	Basic Wall: Exterior Parapet	
	63' - 2 3/4"	1' - 5 1/4"	Basic Wall: Exterior Base	
	62' - 10 3/4"	1' - 1 1/4"	Basic Wall: Exterior Shell	
	62' - 10 3/4"	1' - 1 1/4"	Basic Wall: Exterior Parapet	
	12' - 6 9/16"	1' - 5 1/4"	Basic Wall: Exterior Base	
	12' - 2 9/16"	1' - 1 1/4"	Basic Wall: Exterior Shell	
	12' - 2 9/16"	1' - 1 1/4"	Basic Wall: Exterior Parapet	
	63' - 2 3/4"	1' - 5 1/4"	Basic Wall: Exterior Base	
	62' - 10 3/4"	1' - 1 1/4"	Basic Wall: Exterior Shell	
	62' - 10 3/4"	1' - 1 1/4"	Basic Wall: Exterior Parapet	
	20' - 1 9/16"	1' - 5 1/4"	Basic Wall: Exterior Base	
	19' - 11 9/16"	1' - 1 1/4"	Basic Wall: Exterior Shell	
	19' - 11 9/16"	1' - 1 1/4"	Basic Wall: Exterior Parapet	
	12' - 6 9/16"	1' - 5 1/4"	Basic Wall: Exterior Base	
	12' - 2 9/16"	1' - 1 1/4"	Basic Wall: Exterior Shell	
	12' - 2 9/16"	1' - 1 1/4"	Basic Wall: Exterior Parapet	
	44' - 0"	1' - 5 1/4"	Basic Wall: Exterior Base	
	44' - 0"	1' - 1 1/4"	Basic Wall: Exterior Shell	
	44' - 0"	1' - 1 1/4"	Basic Wall: Exterior Parapet	
	1' - 2 7/8"	1' - 5 1/4"	Basic Wall: Exterior Base	
	1' - 3 1/2"	1' - 1 1/4"	Basic Wall: Exterior Shell	
	1' - 3 1/2"	1' - 1 1/4"	Basic Wall: Exterior Parapet	
	1' - 2 7/8"	1' - 5 1/4"	Basic Wall: Exterior Base	
	1' - 3 1/2"	1' - 1 1/4"	Basic Wall: Exterior Shell	
	1' - 3 1/2"	1' - 1 1/4"	Basic Wall: Exterior Parapet	
D1	14' - 2 3/32"	0' - 6 1/8"	Basic Wall: Interior - 6 1/8" Partition (2-hr)	

Wall Schedule				
Type Mark	Length	Width	Family and Type	Comments
1	59' - 0"	0' - 6 1/8"	Basic Wall: Interior - 6 1/8" Partition (2-hr)	
1	14' - 2 3/32"	0' - 6 1/8"	Basic Wall: Interior - 6 1/8" Partition (2-hr)	
1	21' - 10 3/4"	0' - 6 1/8"	Basic Wall: Interior - 6 1/8" Partition (2-hr)	
1	21' - 10 3/4"	0' - 6 1/8"	Basic Wall: Interior - 6 1/8" Partition (2-hr)	
2	18' - 8"	0' - 5 5/8"	Basic Wall: REA 6" Masonry	
2	18' - 8"	0' - 5 5/8"	Basic Wall: REA 6" Masonry	
1	18' - 8"	1' - 3 5/8"	Basic Wall: REA Shaft Masonry	
2	18' - 8"	0' - 5 5/8"	Basic Wall: REA 6" Masonry	
2	18' - 8"	0' - 5 5/8"	Basic Wall: REA 6" Masonry	
1	18' - 8"	1' - 3 5/8"	Basic Wall: REA Shaft Masonry	
2	18' - 8"	0' - 5 5/8"	Basic Wall: REA 6" Masonry	
2	18' - 8"	0' - 5 5/8"	Basic Wall: REA 6" Masonry	
1	18' - 8"	1' - 3 5/8"	Basic Wall: REA Shaft Masonry	
2	18' - 8"	0' - 5 5/8"	Basic Wall: REA 6" Masonry	
2	18' - 8"	0' - 5 5/8"	Basic Wall: REA 6" Masonry	
1	18' - 8"	1' - 3 5/8"	Basic Wall: REA Shaft Masonry	
2	13' - 2 1/8"	0' - 4 7/8"	Basic Wall: Interior - 4 7/8" Partition (1-hr) A2	
2	12' - 11 11/16"	0' - 4 7/8"	Basic Wall: Interior - 4 7/8" Partition (1-hr) A2	
2	13' - 2 1/8"	0' - 4 7/8"	Basic Wall: Interior - 4 7/8" Partition (1-hr) A2	
2	12' - 11 11/16"	0' - 4 7/8"	Basic Wall: Interior - 4 7/8" Partition (1-hr) A2	
3	7' - 3 11/16"	0' - 4 7/8"	Basic Wall: Interior - 4 7/8" Partition (1-hr) A3	
3	12' - 4 5/8"	0' - 4 7/8"	Basic Wall: Interior - 4 7/8" Partition (1-hr) A3	
1	11' - 10 3/16"	0' - 4 7/8"	Basic Wall: Interior - 4 7/8" Partition (1-hr) A1	
1	6' - 0 1/2"	0' - 4 7/8"	Basic Wall: Interior - 4 7/8" Partition (1-hr) A1	
1	6' - 9 5/8"	0' - 6 1/8"	Basic Wall: Interior - 6 1/8" Partition (2-hr)	
1	41' - 2 1/8"	0' - 6 1/8"	Basic Wall: Interior - 6 1/8" Partition (2-hr)	
2	13' - 7 11/16"	0' - 4 7/8"	Basic Wall: Interior - 4 7/8" Partition (1-hr) A2	
1	24' - 3"	0' - 4 7/8"	Basic Wall: Interior - 4 7/8" Partition (1-hr) A1	
1	13' - 7 11/16"	0' - 4 7/8"	Basic Wall: Interior - 4 7/8" Partition (1-hr) A1	
1	13' - 1 13/16"	0' - 4 7/8"	Basic Wall: Interior - 4 7/8" Partition (1-hr) A1	
1	28' - 11 7/16"	0' - 6 1/8"	Basic Wall: Interior - 6 1/8" Partition (2-hr)	
1	15' - 6 3/32"	0' - 4 7/8"	Basic Wall: Interior - 4 7/8" Partition (1-hr) A1	
1	4' - 10 15/32"	0' - 4 7/8"	Basic Wall: Interior - 4 7/8" Partition (1-hr) A1	
1	6' - 0 1/16"	0' - 4 7/8"	Basic Wall: Interior - 4 7/8" Partition (1-hr) A1	
1	5' - 9 1/16"	0' - 4 7/8"	Basic Wall: Interior - 4 7/8" Partition (1-hr) A1	
1	6' - 8"	0' - 4 7/8"	Basic Wall: Interior - 4 7/8" Partition (1-hr) A1	
1	8' - 0 3/16"	0' - 4 7/8"	Basic Wall: Interior - 4 7/8" Partition (1-hr) A1	
1	2' - 3 5/8"	0' - 4 7/8"	Basic Wall: Interior - 4 7/8" Partition (1-hr) A1	
2	1' - 9 13/16"	0' - 4 7/8"	Basic Wall: Interior - 4 7/8" Partition (1-hr) A2	
2	1' - 10 1/32"	0' - 4 7/8"	Basic Wall: Interior - 4 7/8" Partition (1-hr) A2	
1	14' - 3 5/32"	0' - 4 7/8"	Basic Wall: Interior - 4 7/8" Partition (1-hr) A1	
4	3' - 0 9/16"	0' - 4 1/4"	Basic Wall: Interior - 4 7/8" Partition (1-hr) A4	
4	3' - 5 1/32"	0' - 4 1/4"	Basic Wall: Interior - 4 7/8" Partition (1-hr) A4	
2	1' - 9 3/4"	0' - 4 7/8"	Basic Wall: Interior - 4 7/8" Partition (1-hr) A2	
2	1' - 0 5/16"	0' - 4 7/8"	Basic Wall: Interior - 4 7/8" Partition (1-hr) A2	
1	6' - 5 9/16"	0' - 4 7/8"	Basic Wall: Interior - 4 7/8" Partition (1-hr) A1	
1	6' - 0 1/16"	0' - 4 7/8"	Basic Wall: Interior - 4 7/8" Partition (1-hr) A1	
1	6' - 0 3/8"	0' - 4 7/8"	Basic Wall: Interior - 4 7/8" Partition (1-hr) A1	
1	27' - 10 1/2"	0' - 6 1/8"	Basic Wall: Interior - 6 1/8" Partition (2-hr)	
4	3' - 0 21/32"	0' - 4 1/4"	Basic Wall: Interior - 4 7/8" Partition (1-hr) A4	
4	3' - 7 9/16"	0' - 4 1/4"	Basic Wall: Interior - 4 7/8" Partition (1-hr) A4	



www.paulaubin.com

www.autodesk.com/revit

Consultant
Address
Address
Address
Phone

Printing and Output

15 Commercial Schedules

Project Number	2020.01A
Date	8/1/2020
Drawn By	Author
Checked By	Checker
A603	
Scale	

A603

